


Инв. № подл. 903570
Подп. и дата. Взам. инв. №

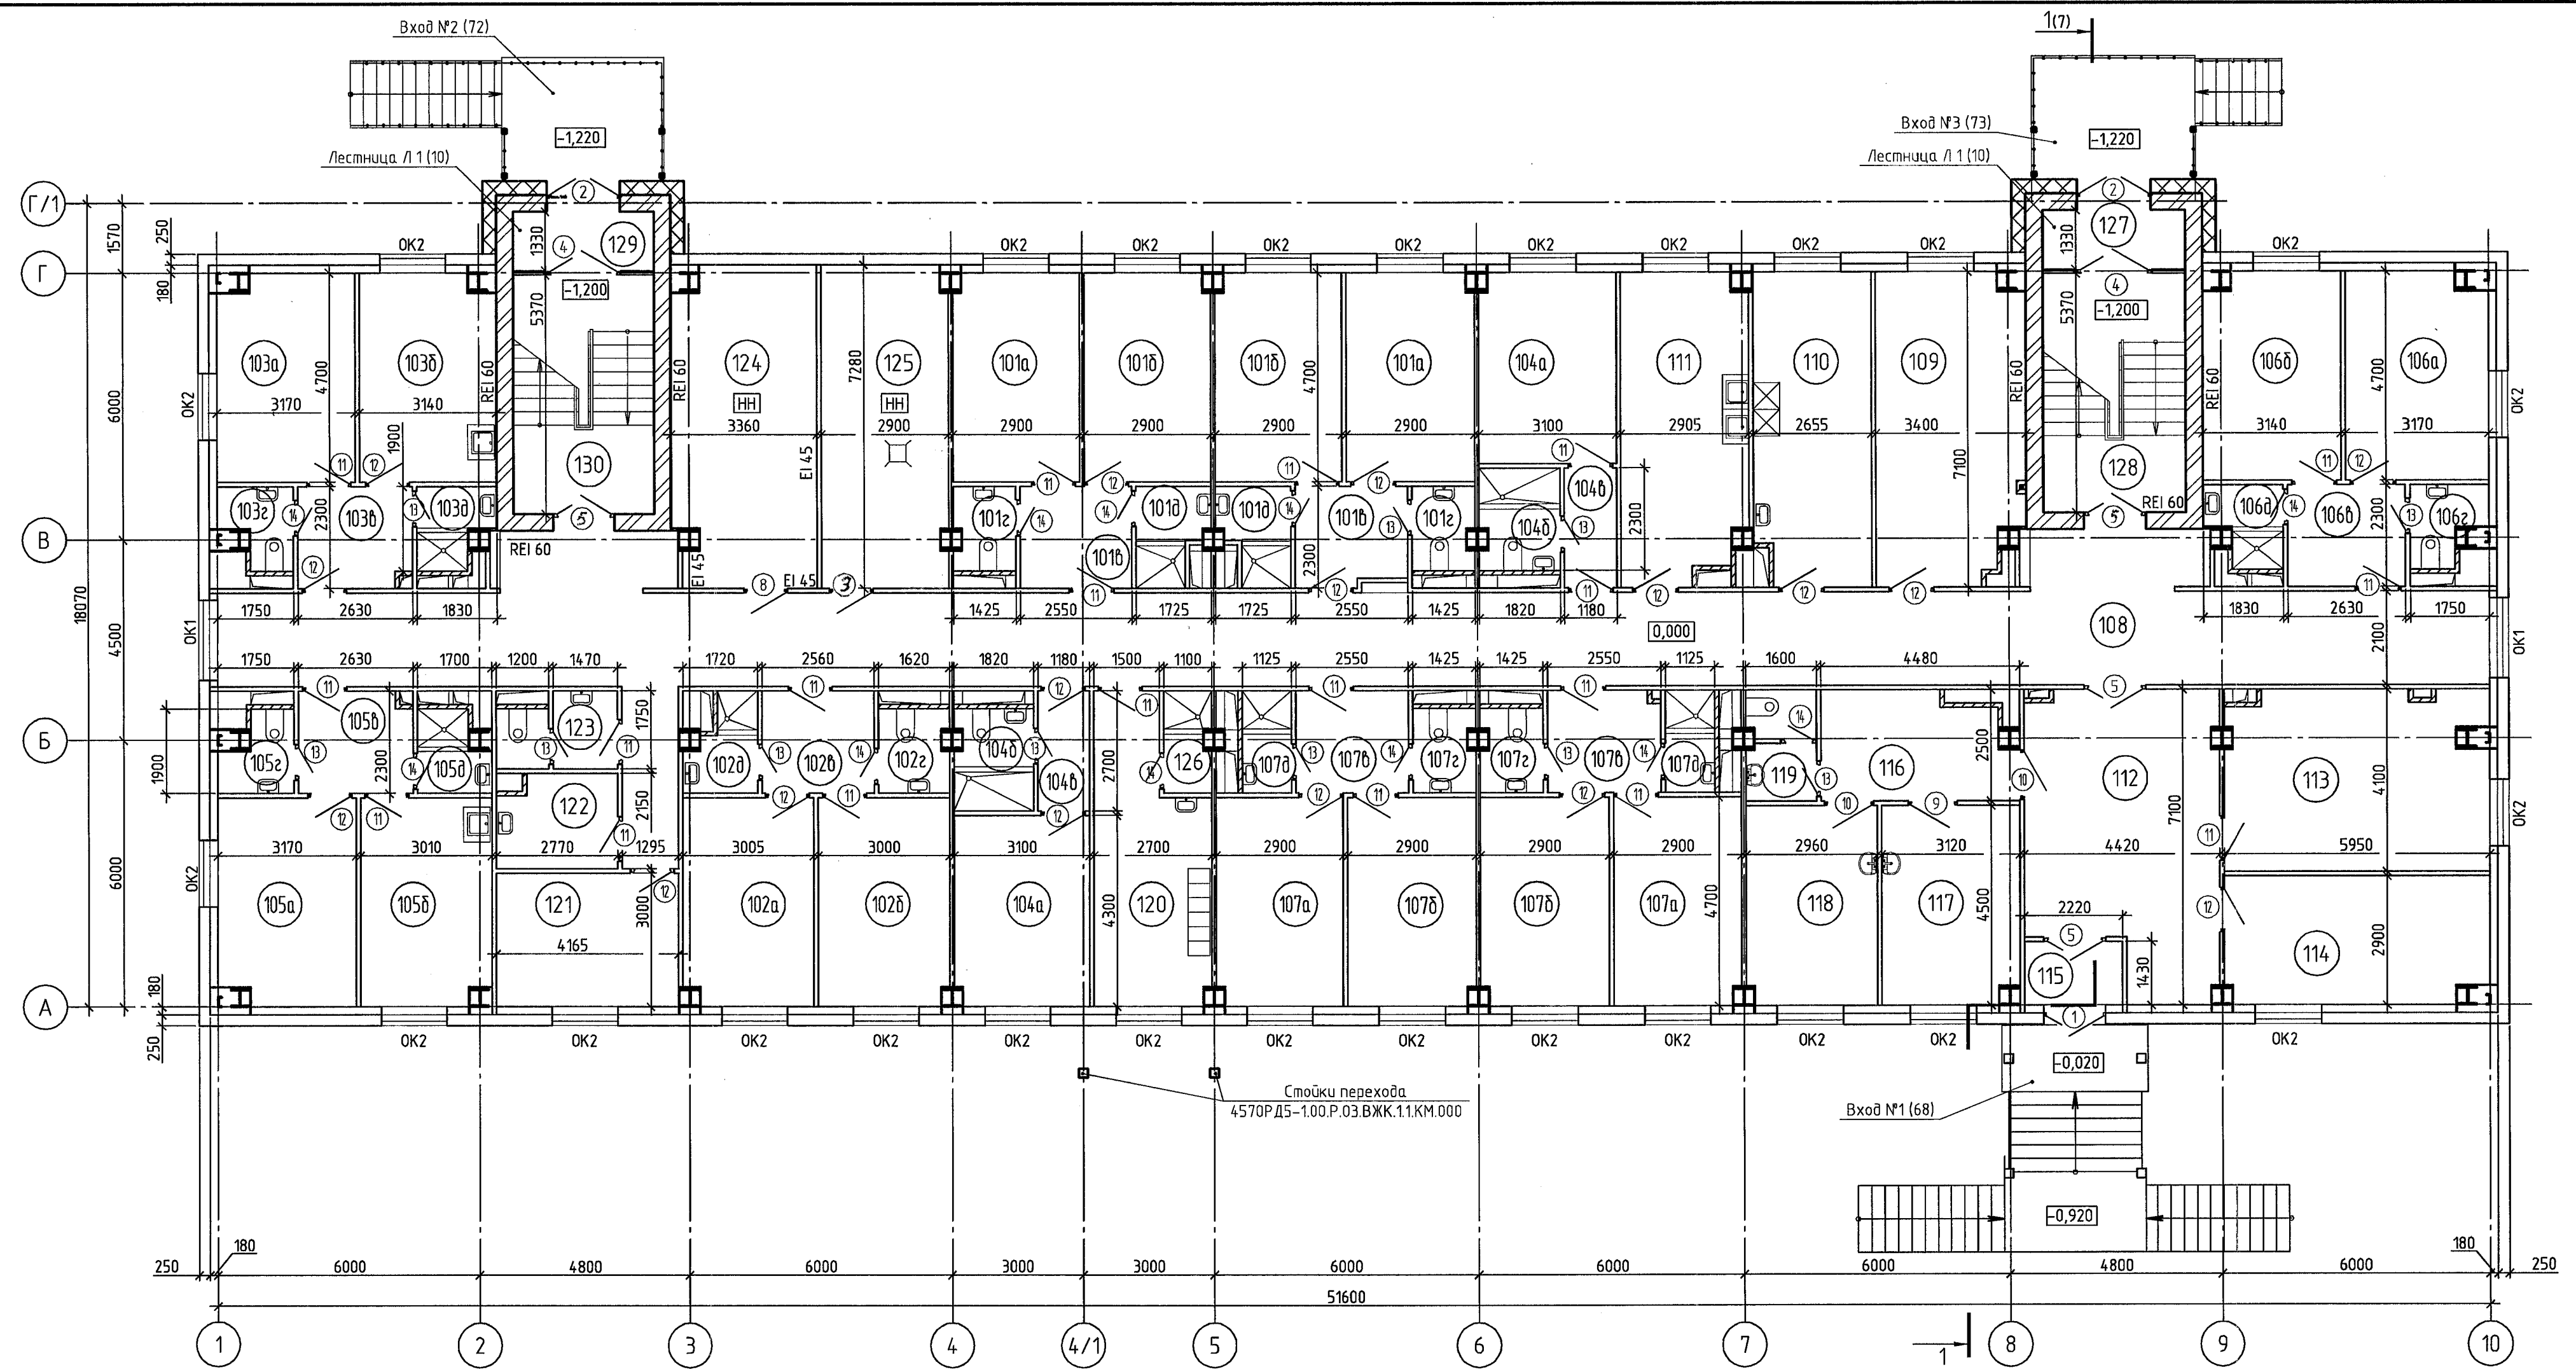

Экспликация помещений			
Номер помещения	Наименование	Площадь, м²	Кат. помещения
Жилая ячейка 2-х комнатная на 4 человека (2шт.)			
101a	Жилая комната на 2 человека	13,5	-
101b	Жилая комната на 2 человека	13,5	-
101c	Прихожая	5,9	-
101d	Уборная	2,6	-
101e	Душевая	3,3	-
Жилая ячейка 2-х комнатная на 4 человека (1шт.)			
102a	Жилая комната на 2 человека	13,9	-
102b	Жилая комната на 2 человека	14,0	-
102c	Прихожая	5,9	-
102d	Уборная	3,0	-
102e	Душевая	3,0	-
Жилая ячейка 2-х комнатная (люкс) на 1 человека (1шт.)			
103a	Жилая комната на 1 человека	14,5	-
103b	Кухня	14,4	-
103c	Прихожая	5,9	-
103d	Уборная	2,6	-
103e	Душевая	2,8	-
Жилая ячейка 1-комнатная на 2 человека (2шт.)			
104a	Жилая комната на 2 человека	13,2	-
104b	Совмещенный санузел	4,1	-
104c	Коридор	3,2	-
Жилая ячейка 2-х комнатная (люкс) на 1 человека (1шт.)			
105a	Жилая комната на 1 человека	14,5	-
105b	Кухня	13,7	-
105c	Прихожая	5,9	-
105d	Уборная	2,6	-
105e	Душевая	2,7	-

Продолжение			
Номер помещения	Наименование	Площадь, м²	Кат. помещения
Жилая ячейка 2-х комнатная на 4 человека (1шт.)			
106a	Жилая комната на 2 человека	14,1	-
106b	Жилая комната на 2 человека	14,4	-
106c	Прихожая	6,0	-
106d	Уборная	2,6	-
106e	Душевая	2,8	-
Жилая ячейка 2-х комнатная на 4 человека (2шт.)			
107a	Жилая комната на 2 человека	13,5	-
107b	Жилая комната на 2 человека	13,5	-
107c	Прихожая	5,9	-
107d	Уборная	2,6	-
107e	Душевая	2,6	-
108	Коридор	124,8	-
109	Помещение сушки одежды и обуви	22,7	-
110	Бытовая комната для стирки, глажки и сушки белья	18,4	-
111	Кухня	19,3	-
112	Вестибюль	27,4	-
113	Помещение для оформления и выдачи путевых документов	23,3	-
114	Помещение заведующего общежитием	16,7	-
115	Тамбур	3,2	-

Оканчание			
Номер помещения	Наименование	Площадь, м²	Кат. помещения
116	Ожидальная	10,0	-
117	Кабинет приема врача	13,8	-
118	Процедурная	13,2	-
119	Уборная	3,9	-
120	Помещение персонала (уборщики служебных и производственных помещений)	16,2	-
121	Помещение технического персонала (сантехник, электрик)	12,3	-
122	Помещение уборочного инвентаря	5,3	-
123	Уборная персонала	4,3	-
124	Помещение электрощитовой	23,1	ВЗ
125	Помещение теплового узла	20,5	Д
126	Душевая	2,4	-
127	Тамбур	4,3	-
128	Лестничная клетка	17,3	-
129	Тамбур	4,3	-
130	Лестничная клетка	17,3	-

* Категория по взрывопожарной и пожарной опасности

Спецификация элементов заполнения проемов и ТТ см. лист 6.

4570РД5-1.00.Р.03.ВЖК.1.1.АС.000					
Магистральный газопровод "Сила Сибири". Этап 5.1. Компрессорная станция КС-1 "Салдыкельская"					
Изм.	Кол. изм.	Лист	№ док.	Подп.	Дата
Разраб.	Сыс. тов.	17.01.19			
Проб.	Кленов	17.01.19			
Гл. спец.	Белов	17.01.19			
Вахтовый жилой комплекс при КС-1 "Салдыкельская". Общежитие на 120 мест				Стадия	Лист
План на отм. 0,000				Р	2
ПАО "ВНИПИгаздобыча"					