


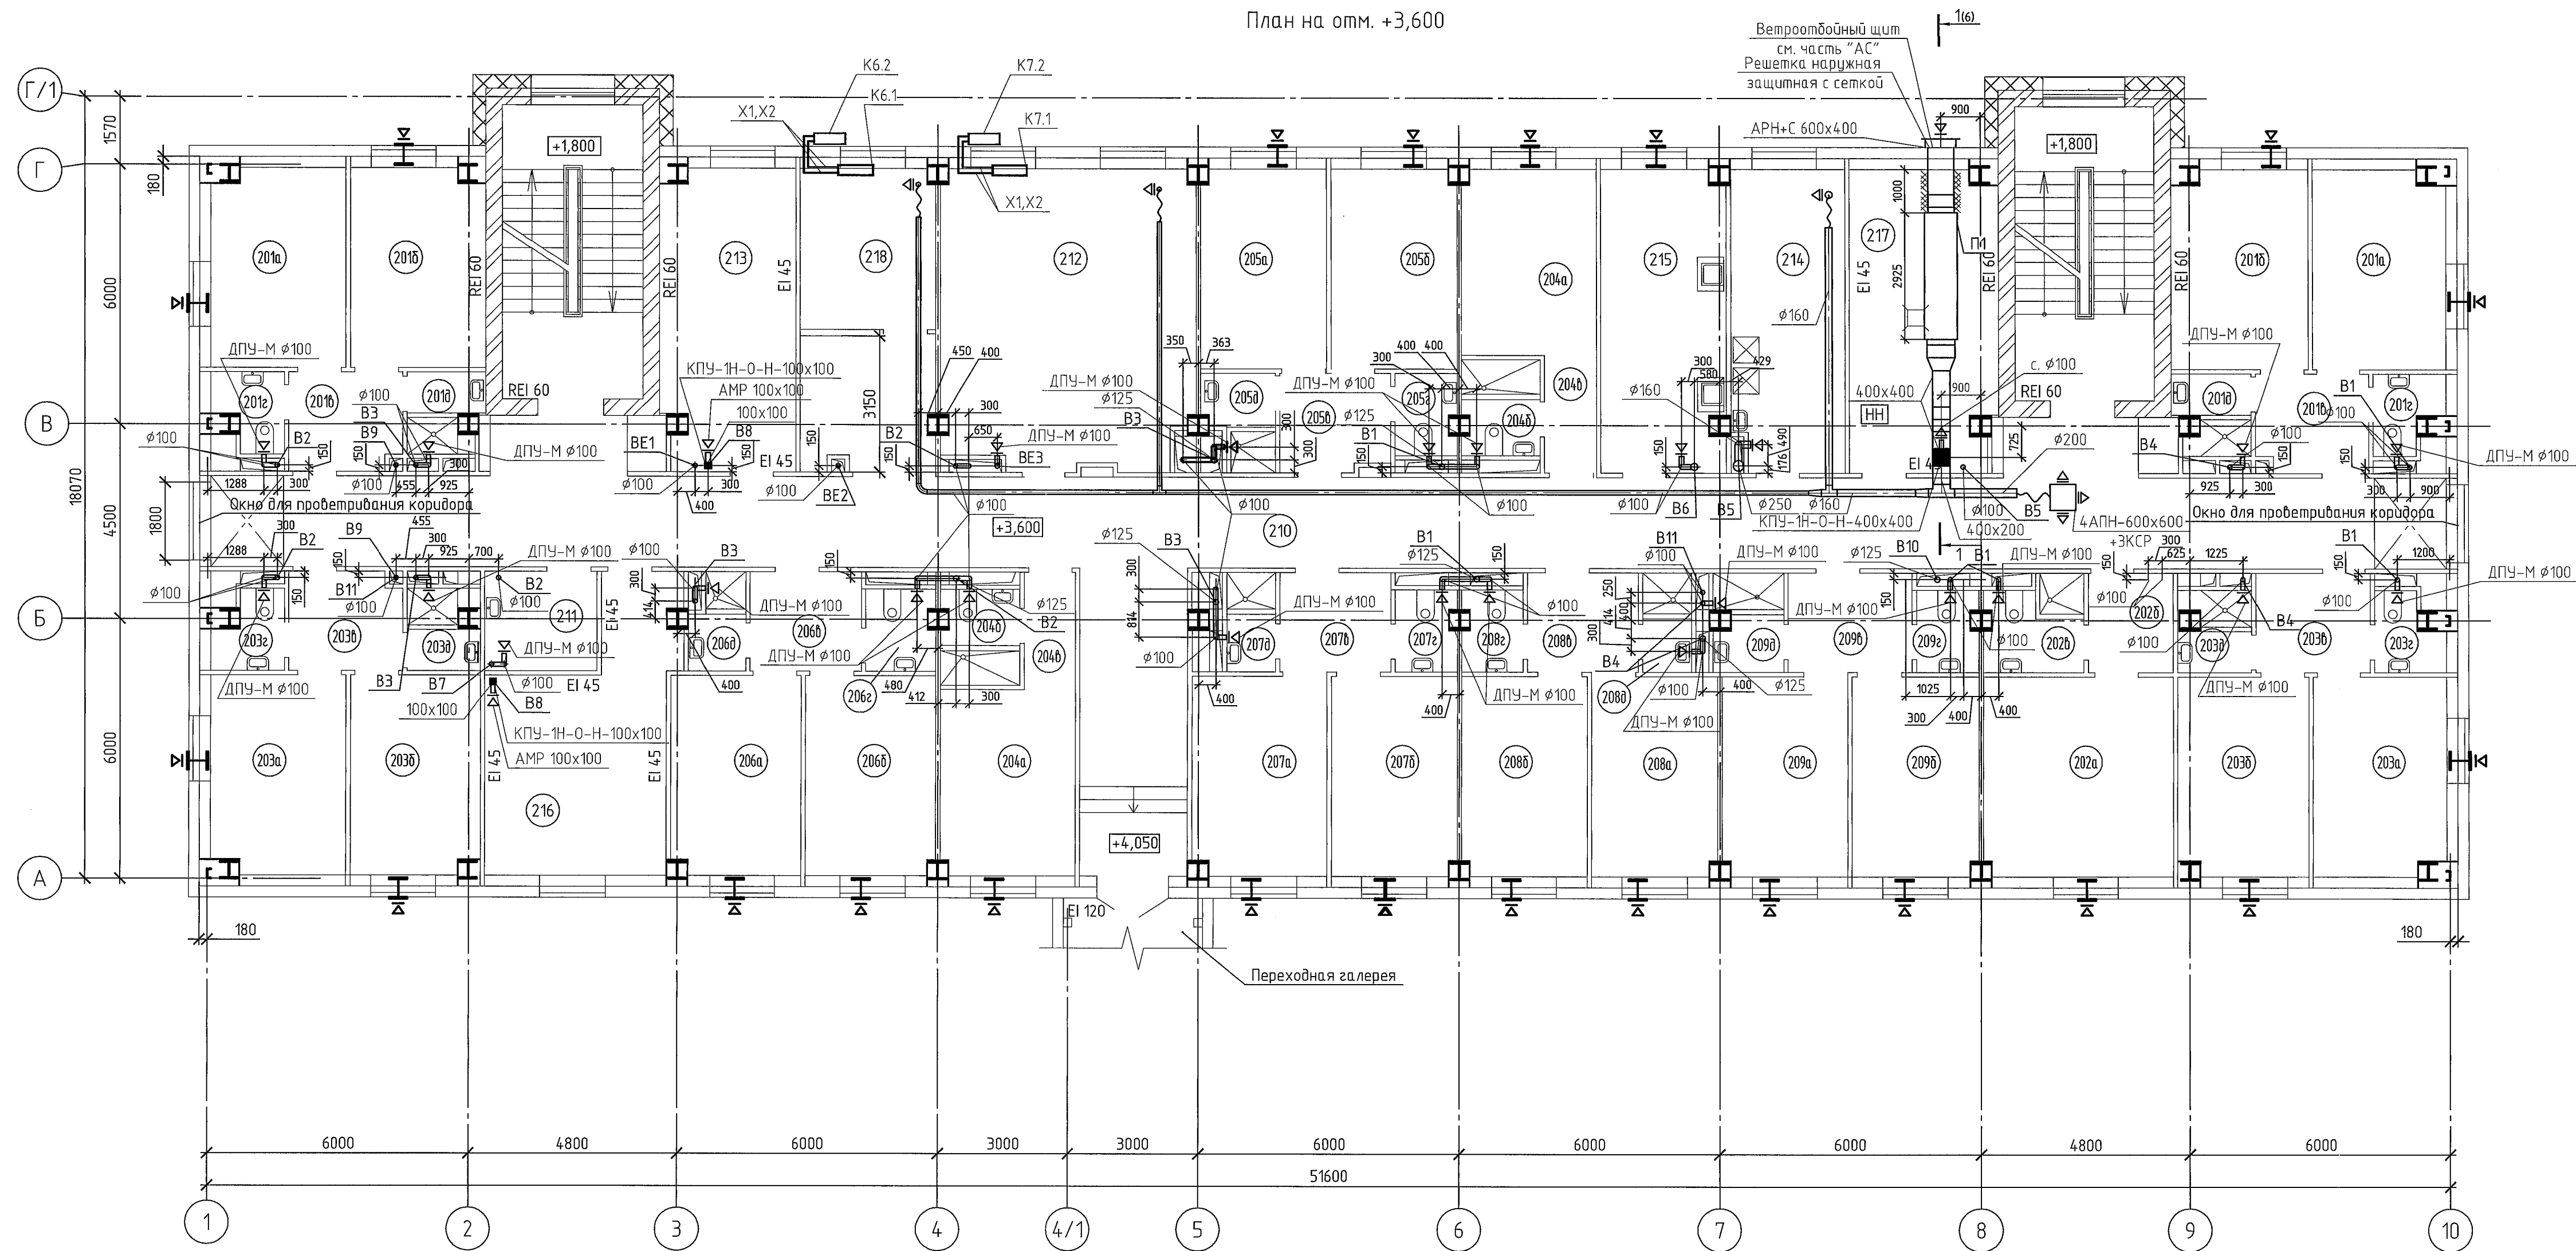

Условные обозначения

Приточный клапан марки Аегесо ЕНА755 с наружным акустическим козырьком А-ЕНА, установленный в переплётах окон в жилых комнатах

1 Степень огнестойкости здания – III
2 Обвязки трубопроводами холодоснабжения X1, X2 между наружным и внутренним блоками сплит-систем K1 – K7 выполнить по месту установки оборудования.

Экспликация помещений

Номер помеще-ния	Наименование	Площадь, м²	Кат. помеще-ния
Жилая ячейка 2-х комнатная на 4 человека (2шт)			
201a	Жилая комната на 2 человека	14,1	-
201б	Жилая комната на 2 человека	14,3	-
201в	Прихожая	5,9	-
201г	Уборная	2,5	-
201д	Душевая	3,0	-
Жилая ячейка 1- комнатная на 2 человека (1шт)			
202a	Жилая комната на 2 человека	20,2	-
202б	Прихожая	4,5	-
202в	Совмещенный санузел	4,8	-
Жилая ячейка 2-х комнатная на 4 человека (2шт)			
203a	Жилая комната на 2 человека	14,1	-
203б	Жилая комната на 2 человека	13,7	-
203в	Прихожая	5,9	-
203г	Уборная	2,5	-
203д	Душевая	3,0	-
Жилая ячейка 1- комнатная на 2 человека (2шт)			
204a	Жилая комната на 2 человека	13,4	-
204б	Совмещенный санузел	3,9	-
204в	Прихожая	3,1	-
Жилая ячейка 2-х комнатная на 4 человека (1шт)			
205a	Жилая комната на 2 человека	13,3	-
205б	Жилая комната на 2 человека	13,3	-
205в	Прихожая	5,7	-
205г	Уборная	2,6	-
205д	Душевая	3,3	-
Жилая ячейка 2-х комнатная на 4 человека (1шт)			
206a	Жилая комната на 2 человека	13,7	-
206б	Жилая комната на 2 человека	13,8	-
206в	Прихожая	5,9	-
206г	Уборная	3,0	-
206д	Душевая	2,6	-

Окончание

Номер помеще-ния	Наименование	Площадь, м²	Кат. помеще-ния
Жилая ячейка 2-х комнатная на 4 человека (1шт)			
207a	Жилая комната на 2 человека	14,2	-
207б	Жилая комната на 2 человека	13,3	-
207в	Прихожая	5,9	-
207г	Уборная	2,6	-
207д	Душевая	2,6	-
Жилая ячейка 2-х комнатная на 4 человека (1шт)			
208a	Жилая комната на 2 человека	13,3	-
208б	Жилая комната на 2 человека	13,3	-
208в	Прихожая	5,9	-
208г	Уборная	2,6	-
208д	Душевая	2,6	-
Жилая ячейка 2-х комнатная на 4 человека (1шт)			
209a	Жилая комната на 2 человека	13,3	-
209б	Жилая комната на 2 человека	13,3	-
209в	Прихожая	6,6	-
209г	Уборная	2,6	-
209д	Душевая	3,5	-
210	Коридор	147,3	-
211	Помещение уборочного инвентаря	5,9	-
212	Комната для отдыха	39,8	-
213	Кладовая мебели	21,3	B3
214	Бытовая комната для стирки, глажки и сушки белья	18,4	-
215	Кухня	20,1	-
216	Кладовая грязного белья	23,6	B3
217	Помещение приточной вентиляционной камеры	23,1	B4
218	Помещение кастиляши	11,5	-

* Категория по взрывопожарной и пожарной опасности

4570PД5-1.00.P.03.BЖК.1.10B.000					
Магистральный газопровод "Сила Сибири". Этап 5.1. Компрессорная станция КС-1 "Салдыкельская"					
Изм.	Кол. изм.	Лист	№ док.	Подп.	Дата
Разработал	Продумал	Проверил	Букин	Неплюдов	Гл. спец.
Важный жилой комплекс при КС-1 "Салдыкельская". Общежитие на 120 мест				Р	З
Вентиляция. План на отм. +3,600				ПАО "ВНИПИгаздобыча"	