


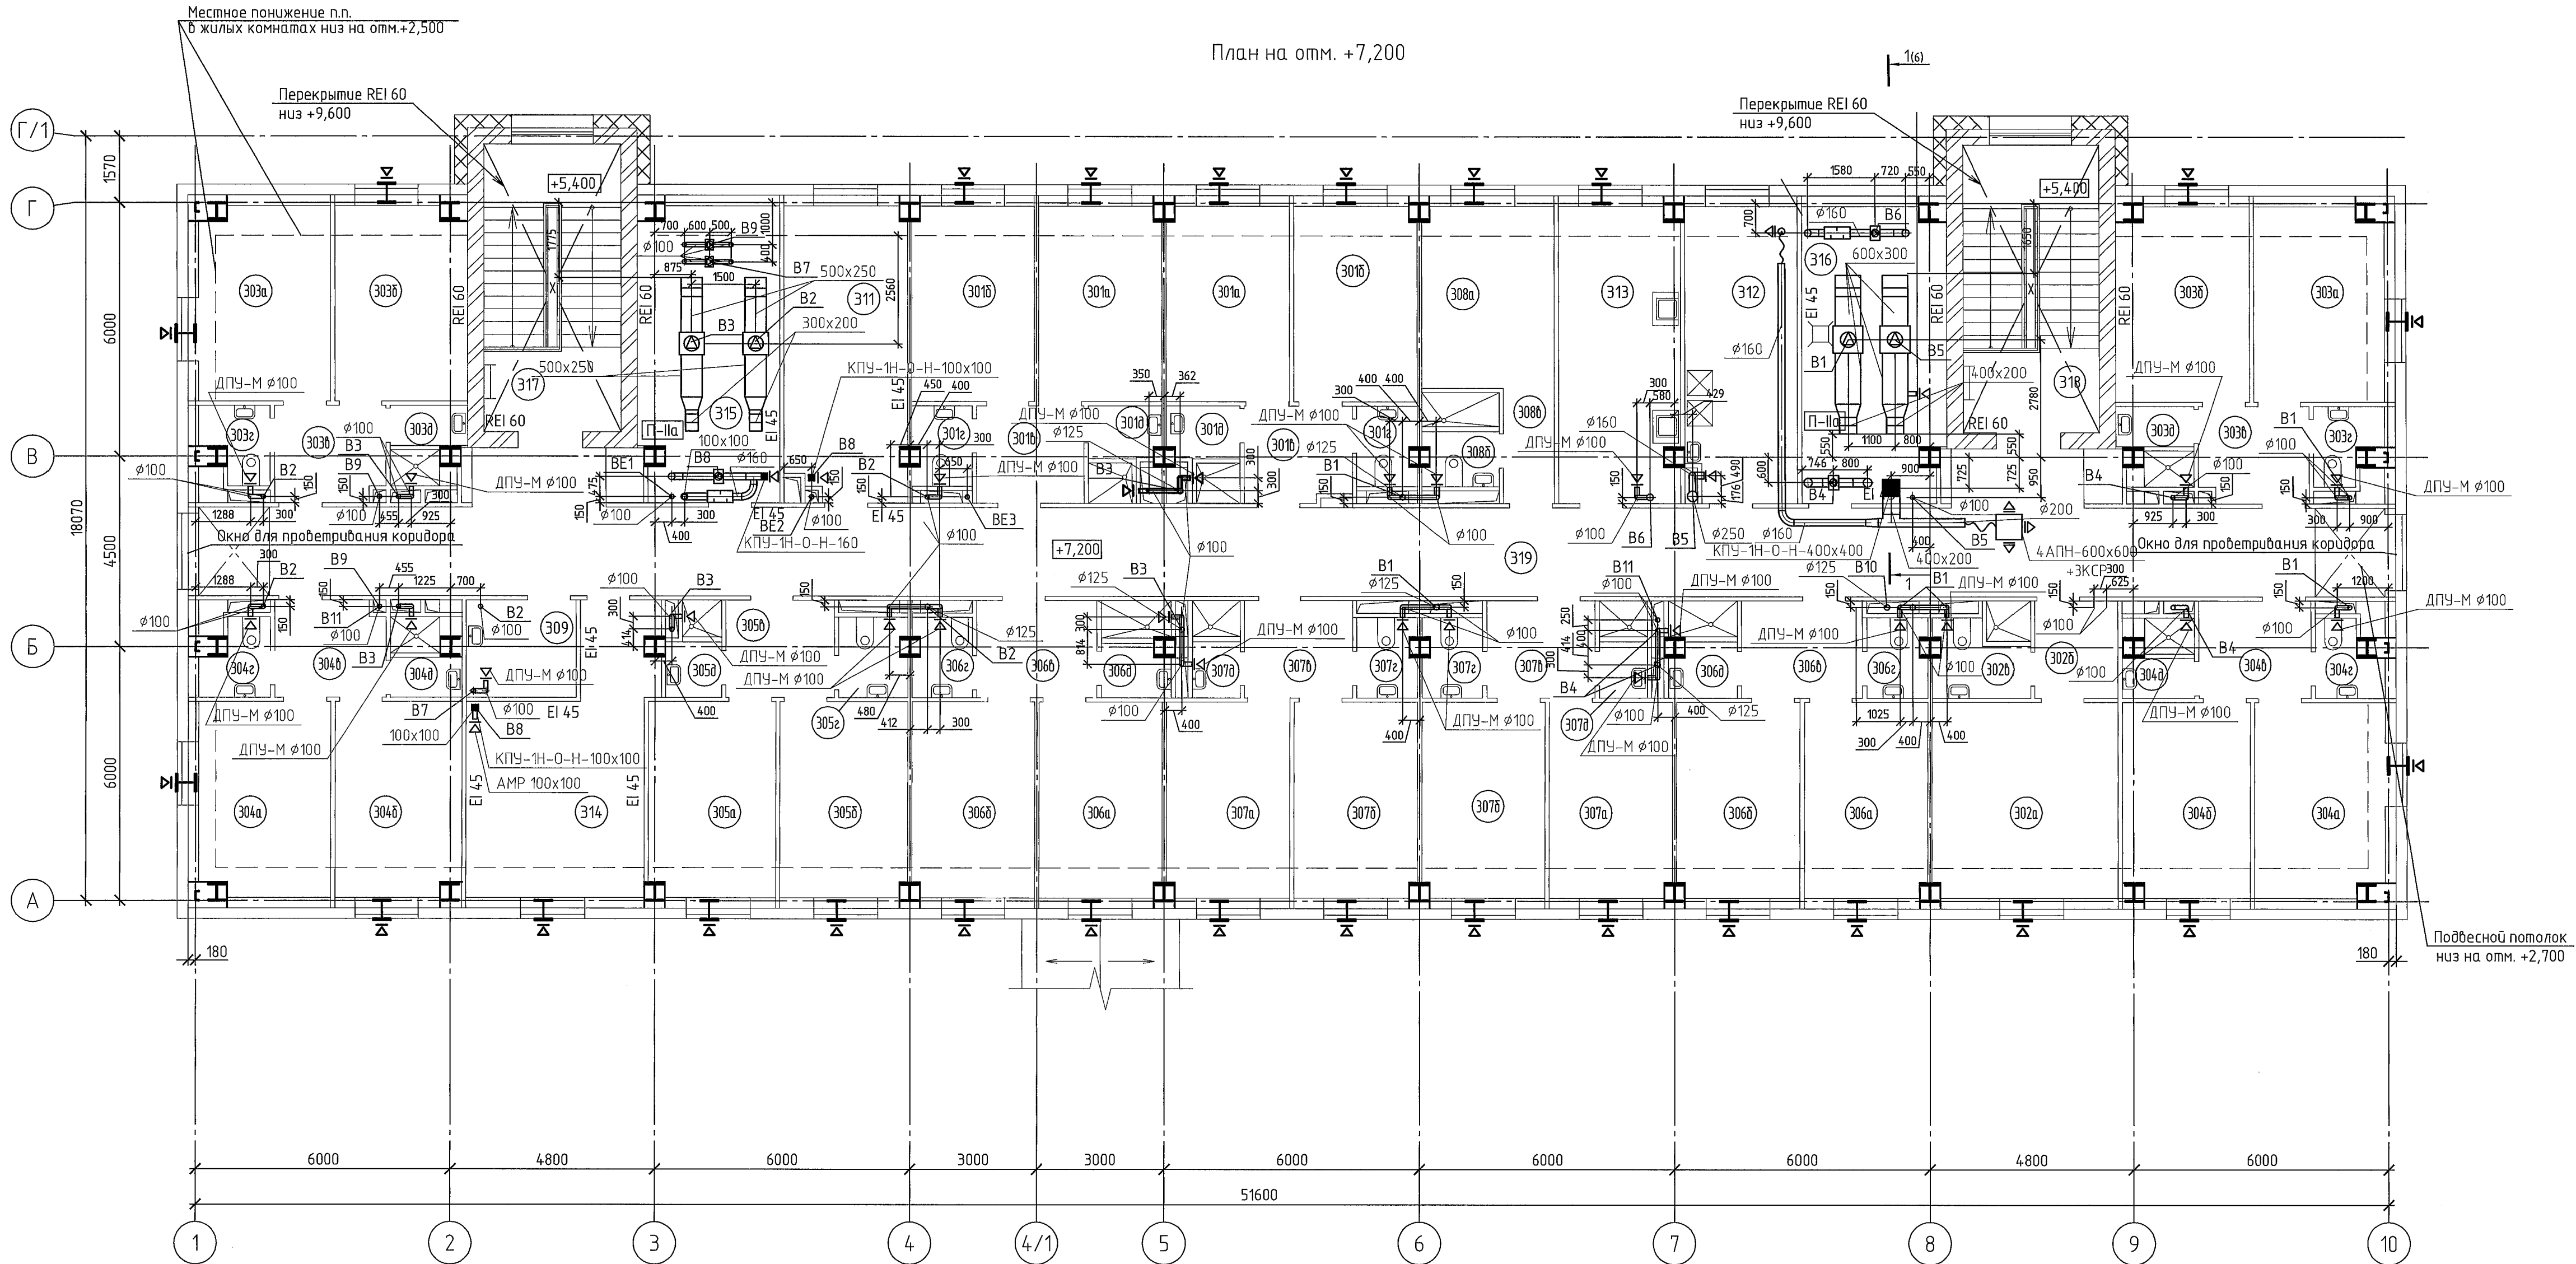

Условные обозначения

Приточный клапан марки Aerugo EHA755 с наружным акустическим козырьком А-ЕНА, установленный в переплетах окон в жилых комнатах

1 Степень огнестойкости здания – III
2 Обвязку трубопроводами холодоснабжения Х1, Х2 между наружным и внутренним блоками сплит-систем К1 – К7 выполнить по месту установкой оборудования.

Экспликация помещений

Номер помещения	Наименование	Площадь, м²	Кат. помещения
Жилая ячейка 2-х комнатная на 4 человека (2шт)			
301a	Жилая комната на 2 человека	13,3	-
301б	Жилая комната на 2 человека	13,3	-
301в	Прихожая	5,9	-
301г	Уборная	2,6	-
301д	Душевая	3,3	-
Жилая ячейка 1- комнатная на 2 человека (1шт)			
302a	Жилая комната на 2 человека	20,2	-
302б	Прихожая	4,5	-
302в	Совмещенный санузел	4,8	-
Жилая ячейка 2-х комнатная на 4 человека (2шт)			
303a	Жилая комната на 2 человека	14,1	-
303б	Жилая комната на 2 человека	14,3	-
303в	Прихожая	5,9	-
303г	Уборная	2,5	-
303д	Душевая	3,0	-
Жилая ячейка 2-х комнатная на 4 человека (2шт)			
304a	Жилая комната на 2 человека	14,1	-
304б	Жилая комната на 2 человека	13,7	-
304в	Прихожая	5,9	-
304г	Уборная	2,5	-
304д	Душевая	2,9	-
Жилая ячейка 2-х комнатная на 4 человека (1шт)			
305a	Жилая комната на 2 человека	13,7	-
305б	Жилая комната на 2 человека	13,8	-
305в	Прихожая	5,9	-
305г	Уборная	3,0	-
305д	Душевая	2,6	-

Окончание

Номер помещения	Наименование	Площадь, м²	Кат. помещения
Жилая ячейка 2-х комнатная на 4 человека (2шт)			
306a	Жилая комната на 2 человека	13,3	-
306б	Жилая комната на 2 человека	13,3	-
306в	Прихожая	6,6	-
306г	Уборная	2,6	-
306д	Душевая	3,5	-
Жилая ячейка 2-х комнатная на 4 человека (2шт)			
307a	Жилая комната на 2 человека	13,3	-
307б	Жилая комната на 2 человека	13,3	-
307в	Прихожая	5,9	-
307г	Уборная	2,6	-
307д	Душевая	2,6	-
Жилая ячейка 1- комнатная на 2 человека (1шт)			
308a	Жилая комната на 2 человека	3,4	-
308б	Совмещенный санузел	3,9	-
308в	Прихожая	3,2	-
Жилая ячейка 2-х комнатная на 4 человека (2шт)			
309	Помещение уборочного инвентаря	5,9	-
310	Помещение связи	21,0	-
311	Кладовая личных вещей проживающих	19,8	ВЗ
312	Бытовая комната для стирки, глажки и сушки белья	18,2	-
313	Кухня	19,9	-
314	Кладовая чистого белья	23,6	ВЗ
315	Помещение вытяжной венткамеры	22,8	ВЗ
316	Помещение вытяжной венткамеры	23,1	ВЗ
317	Лестничная клетка	21,9	-
318	Лестничная клетка	21,9	-
319	Коридор	119,8	-

* Категория по взрывопожарной и пожарной опасности

4570P.D5-1.00.P.03.BЖК.1.1.0B.000

Магистральный газопровод "Сила Сибири".
Этап 5.1. Компрессорная станция КС-1 "Салдыкельская"

Изм.	Кол. изм.	Лист	№ док.	Подп.	Дата
Разработал	Продумал	Проверил	Букин	Непилювич	2024.08.01
Гл. спец.					

Вахтовый жилой комплекс при КС-1 "Салдыкельская".
Общедомовые на 120 мест

Стация	Лист	Листов
Р	4	

Вентиляция. План на отм. +7,200

ПАО "ВНИПИгаздобыча"