


План чердака (неотапливаемого)

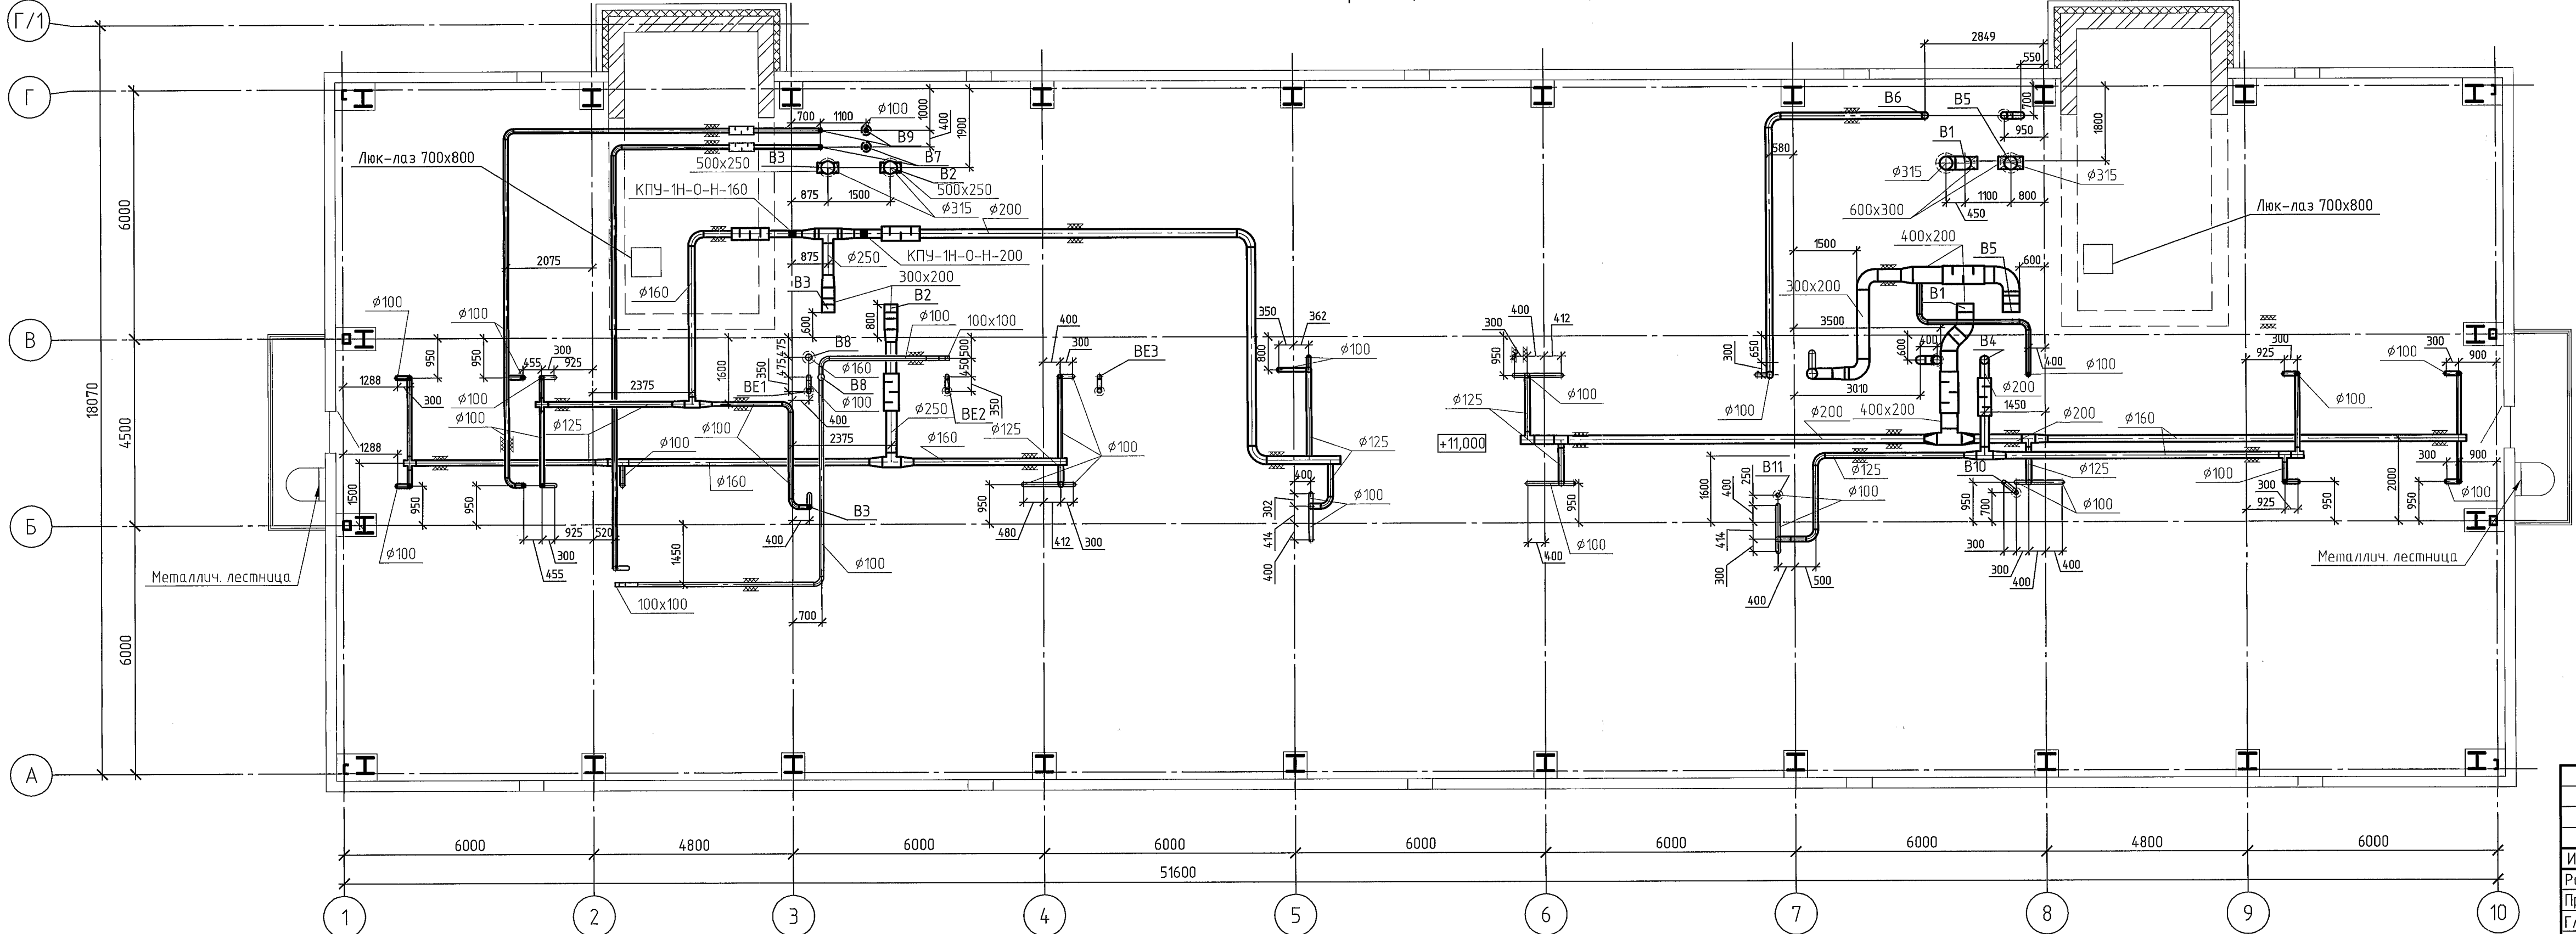

Все воздуховоды, расположенные на чердаке, выполнены из стали $\delta=1,2$ мм на сварке и покрыты тепловой изоляцией, обеспечивающей предел огнестойкости EI30.

4570PД5-1.00.Р.03.ВЖК.1.1.0В.000					
Магистральный газопровод "Сила Сибири". Этап 5.1. Компрессорная станция КС-1 "Салдыкельская"					
Изм.	Кол. изм.	Лист	№ док.	Подп.	Дата
Разработал	Прудников				20.11.18
Проверил	Букин				20.11.18
Гл. спец.	Нелипович				20.11.18
Вахтовый жилой комплекс при КС-1 "Салдыкельская". Общедомовое на 120 мест				Стадия	Лист
Вентиляция. План чердака (неотапливаемого)				Р	5
				Листов	
				ПАС "ВНИПИгаздобыча"	

Инд. № подл. 900581
Подп. и дата. Взам. инв. №