
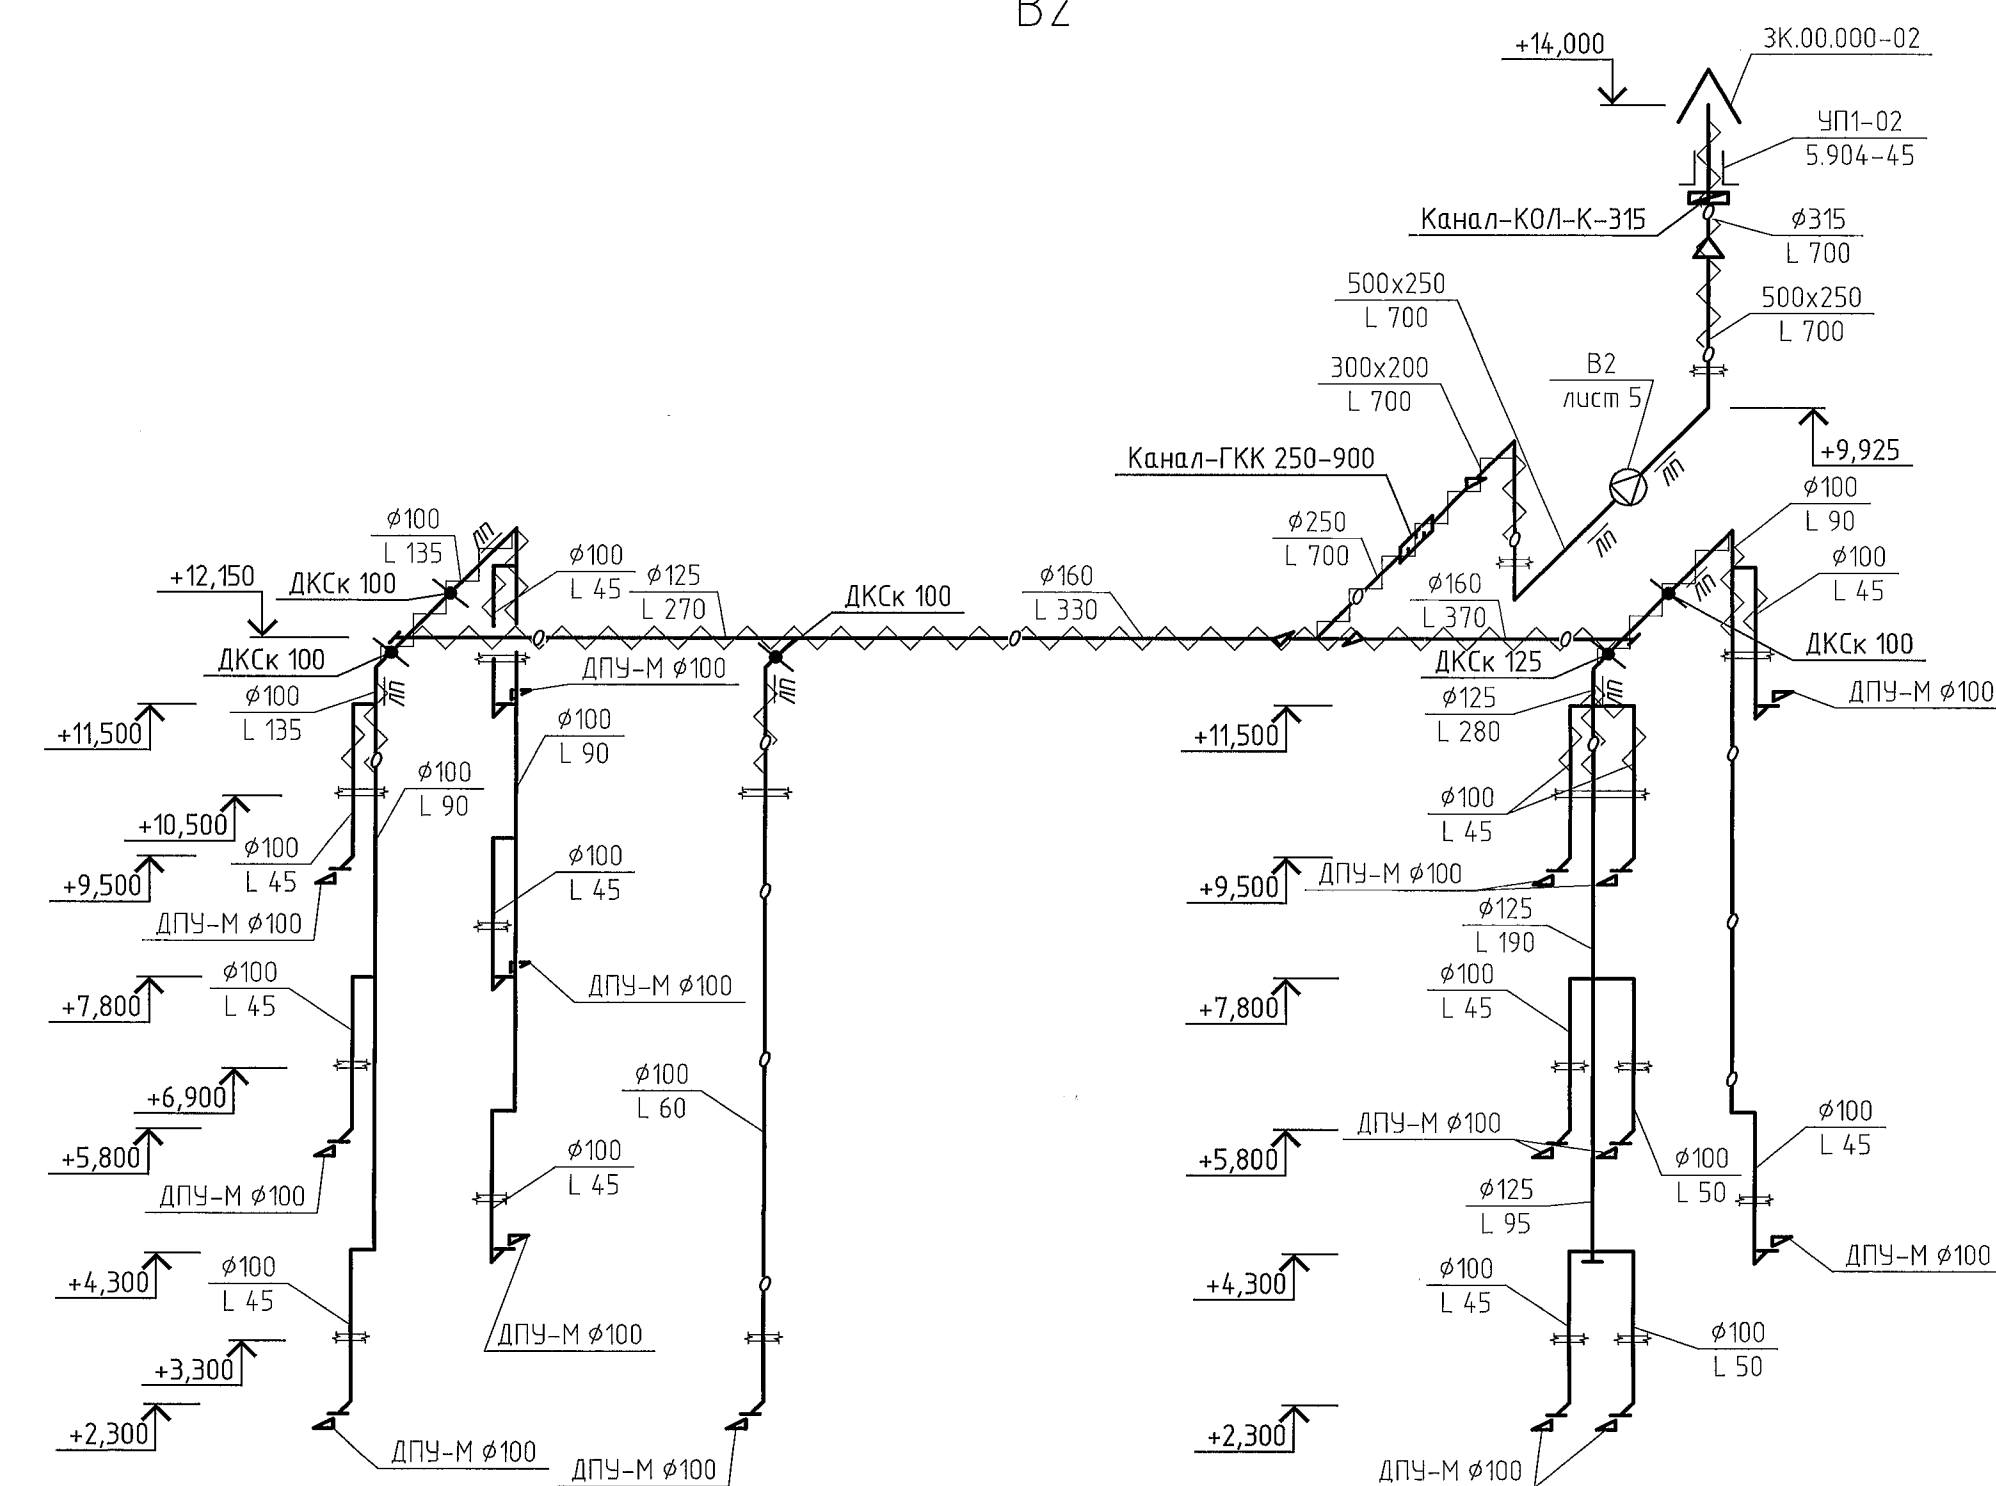
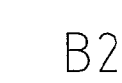
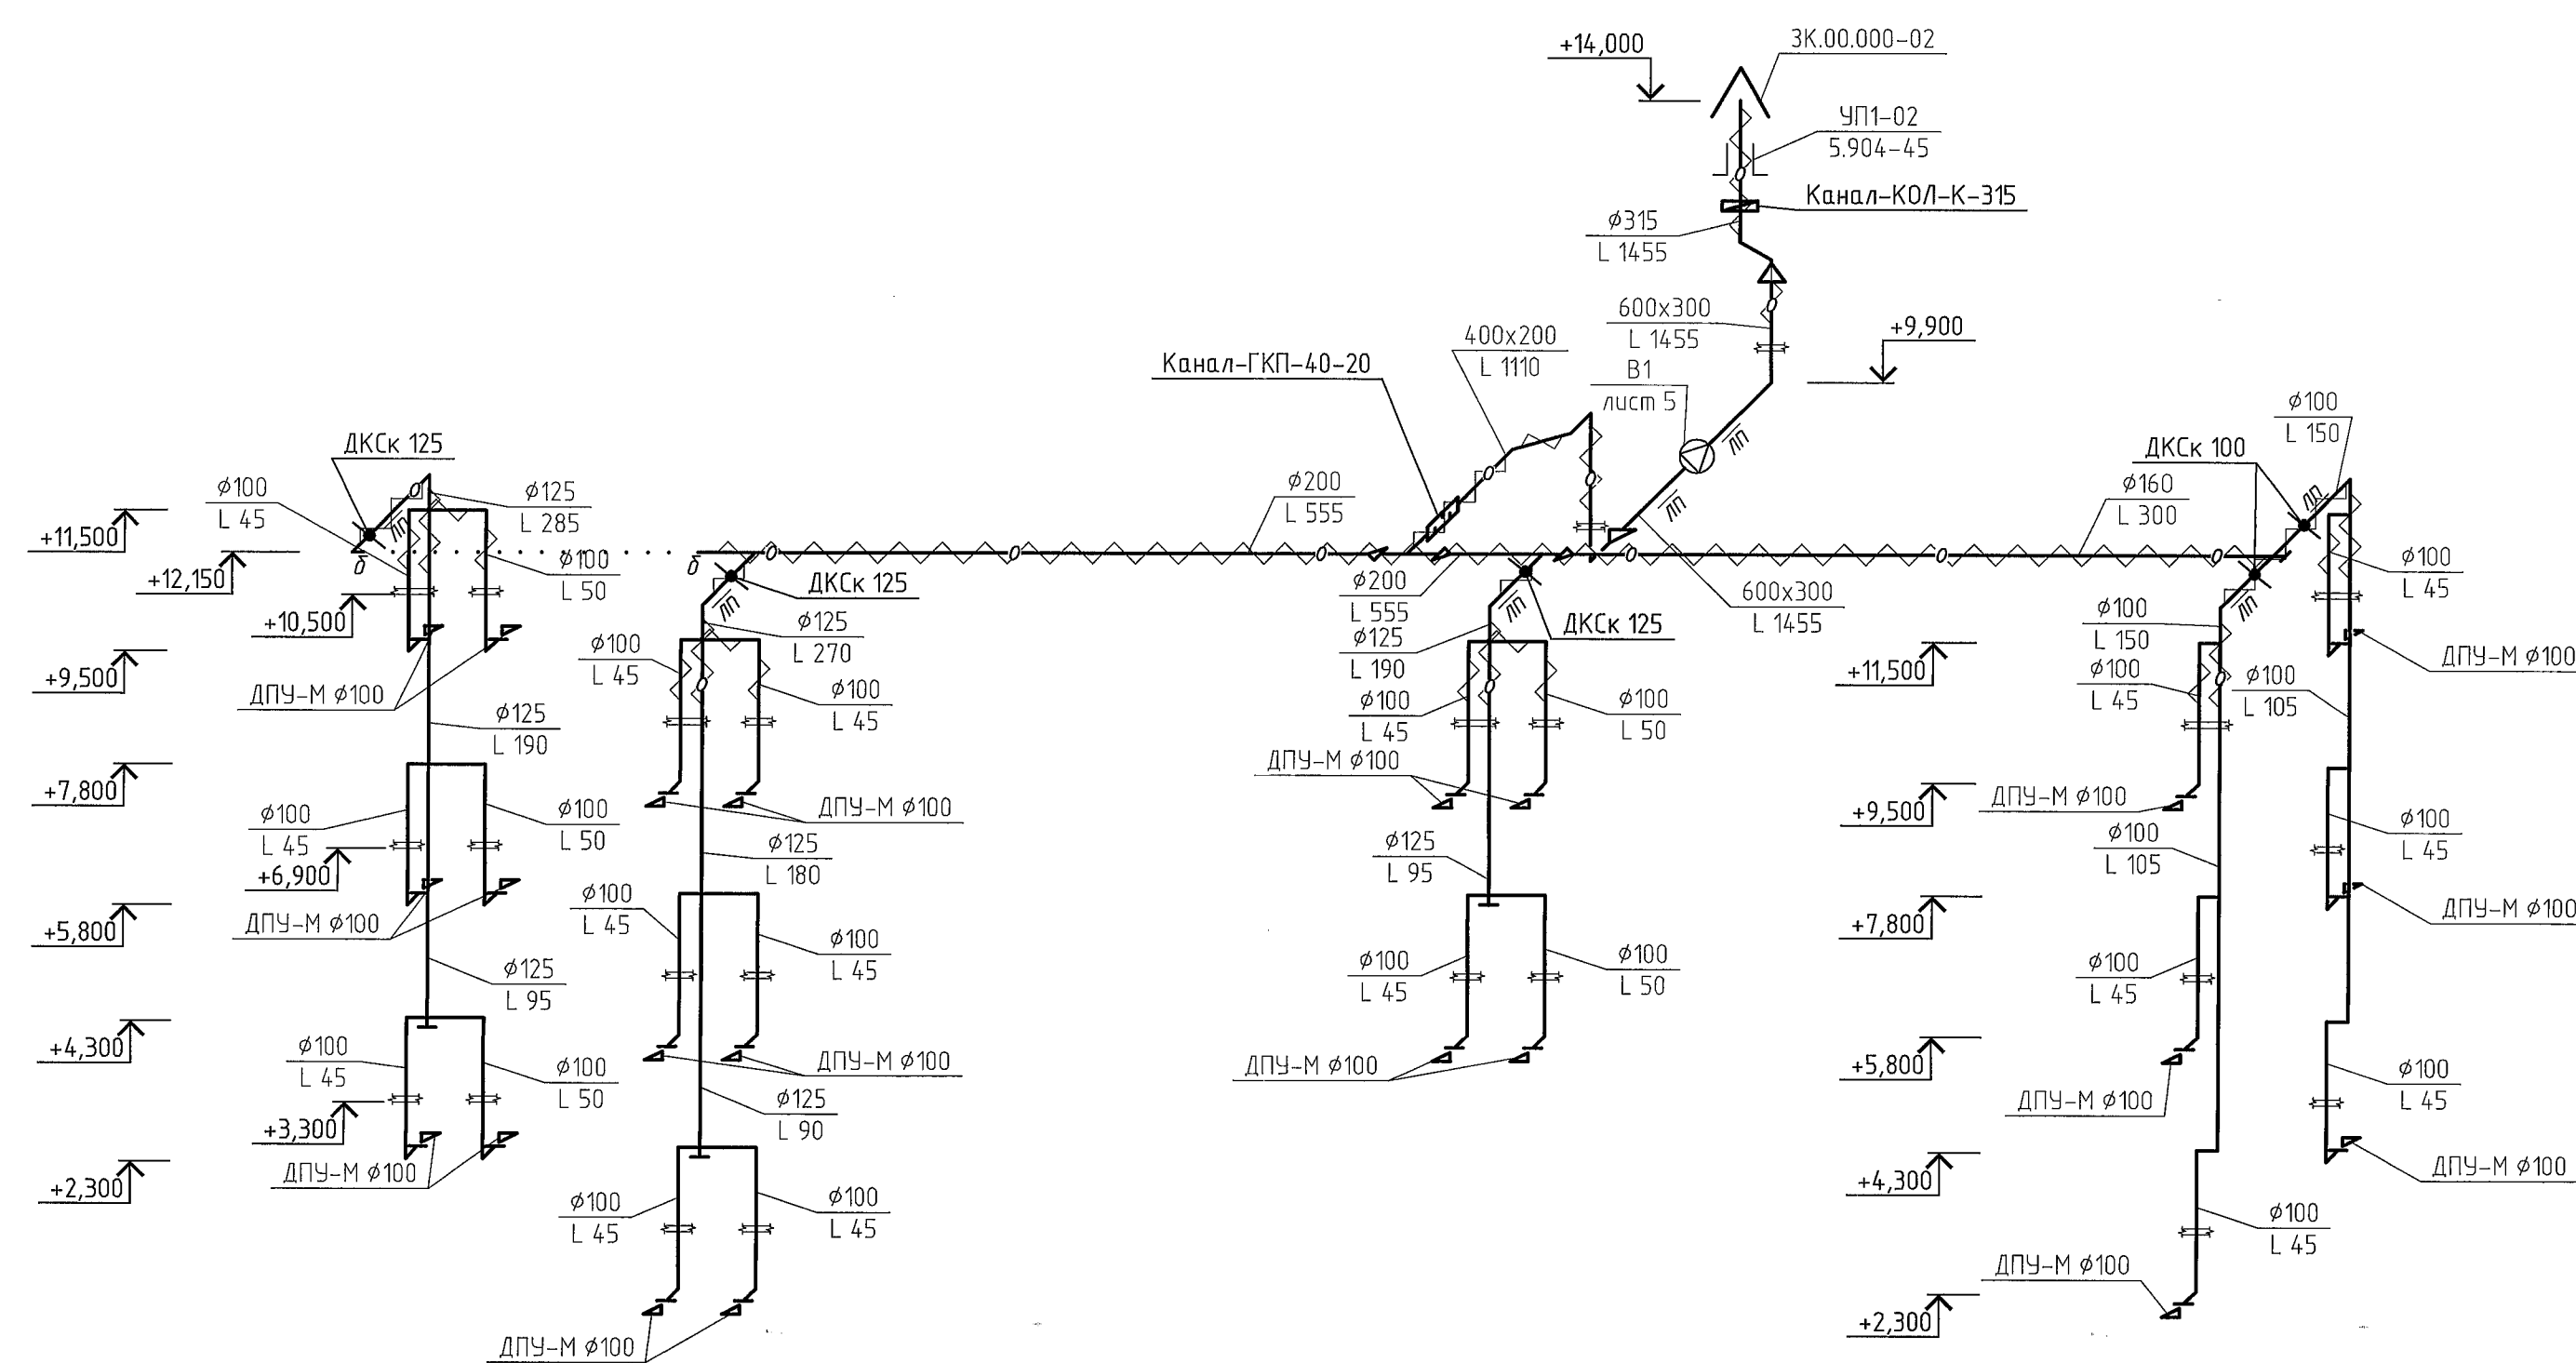
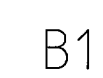
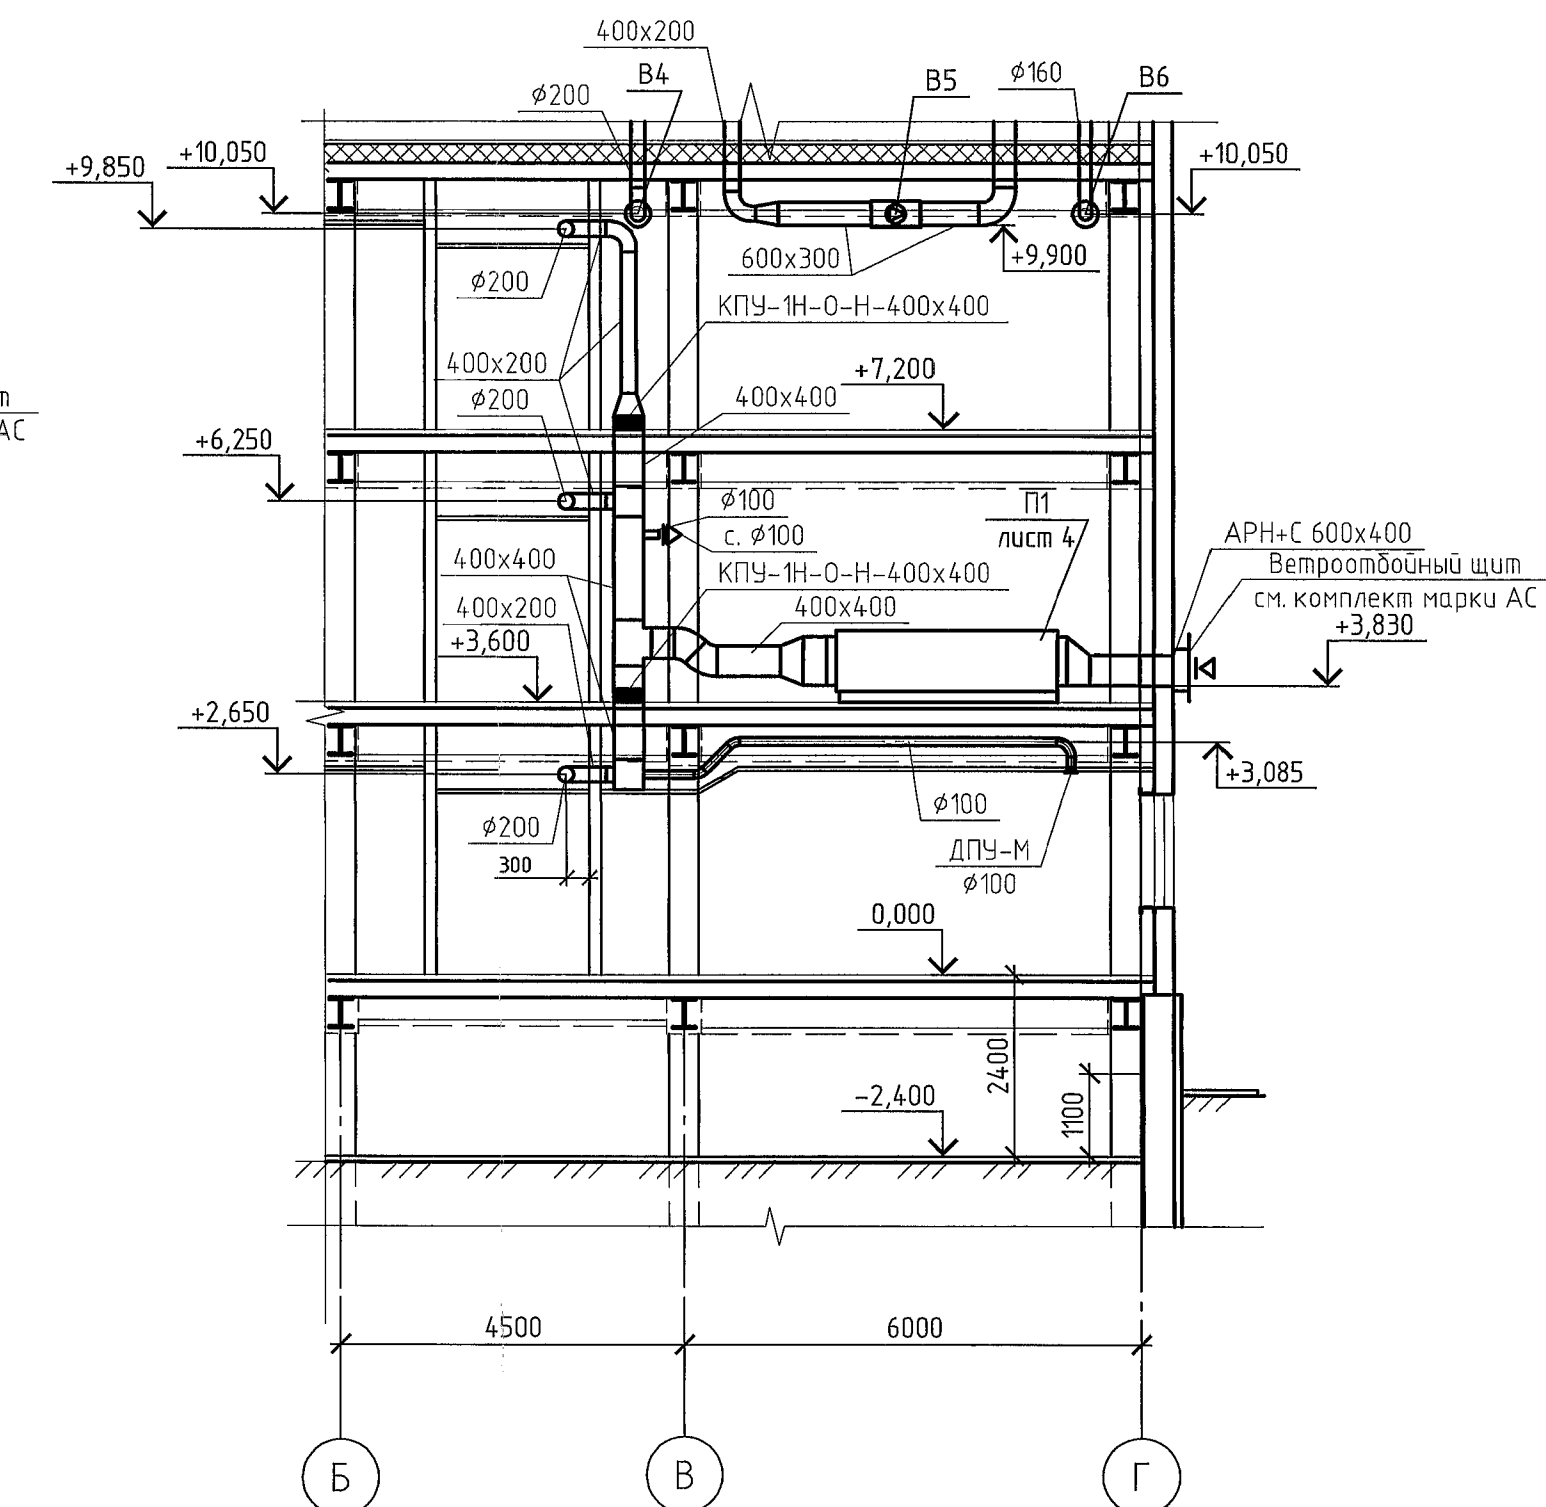
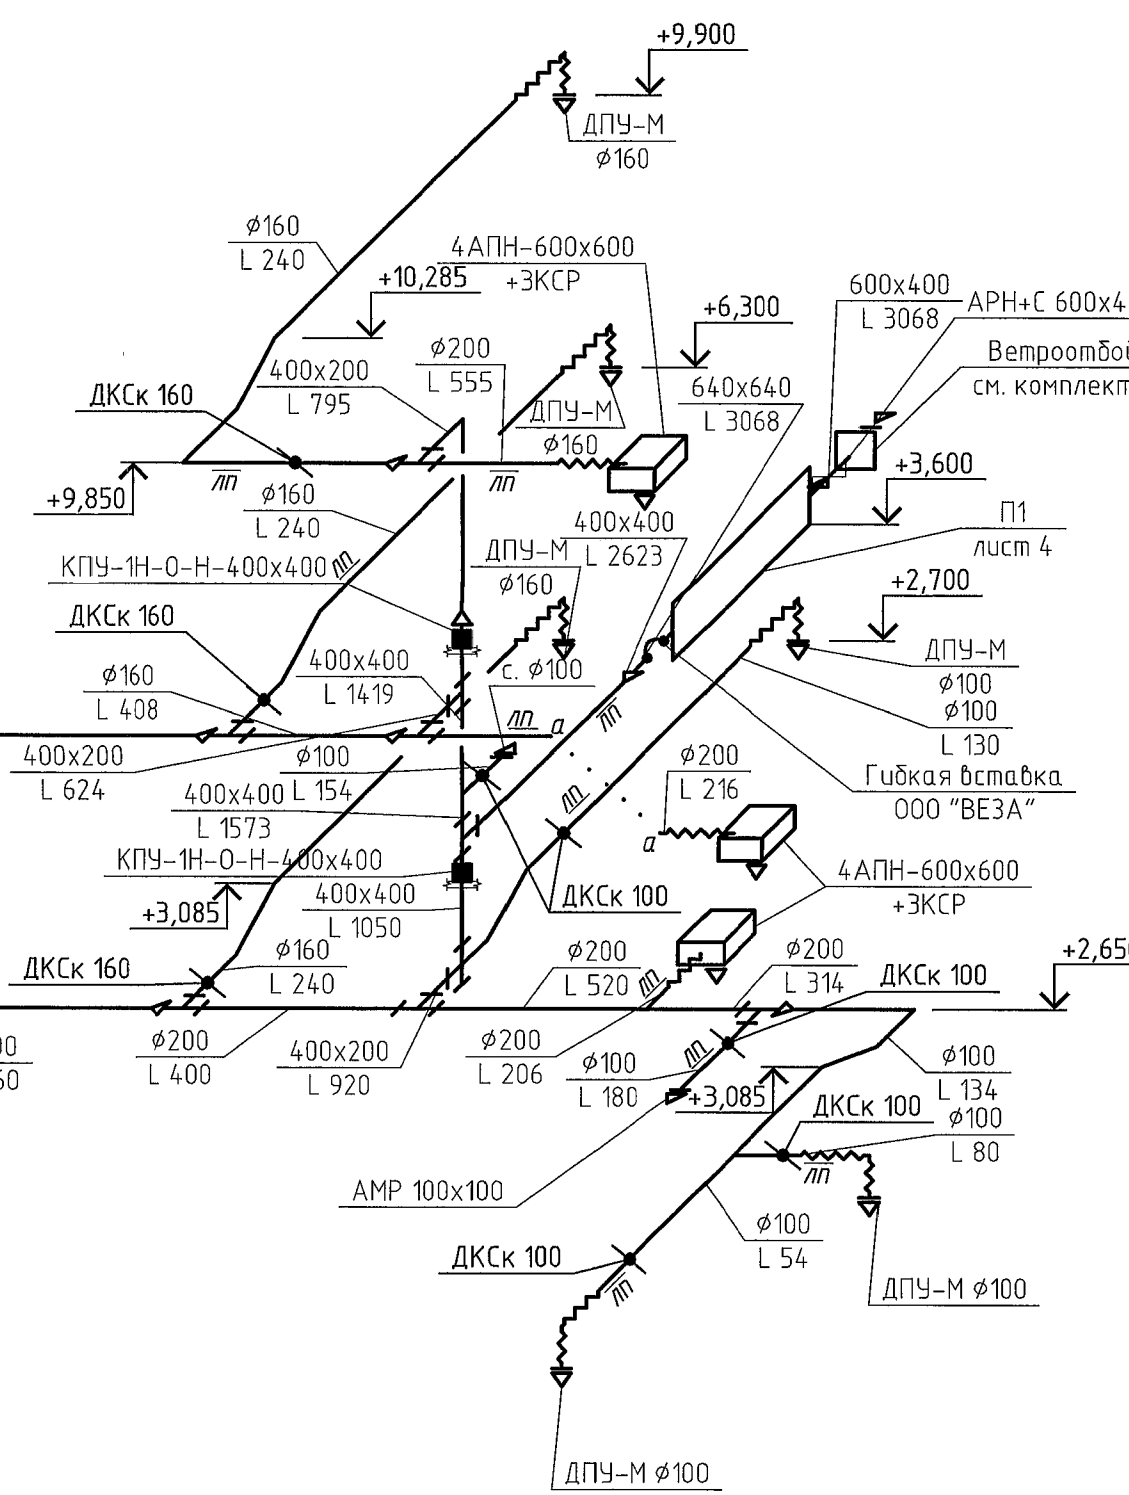
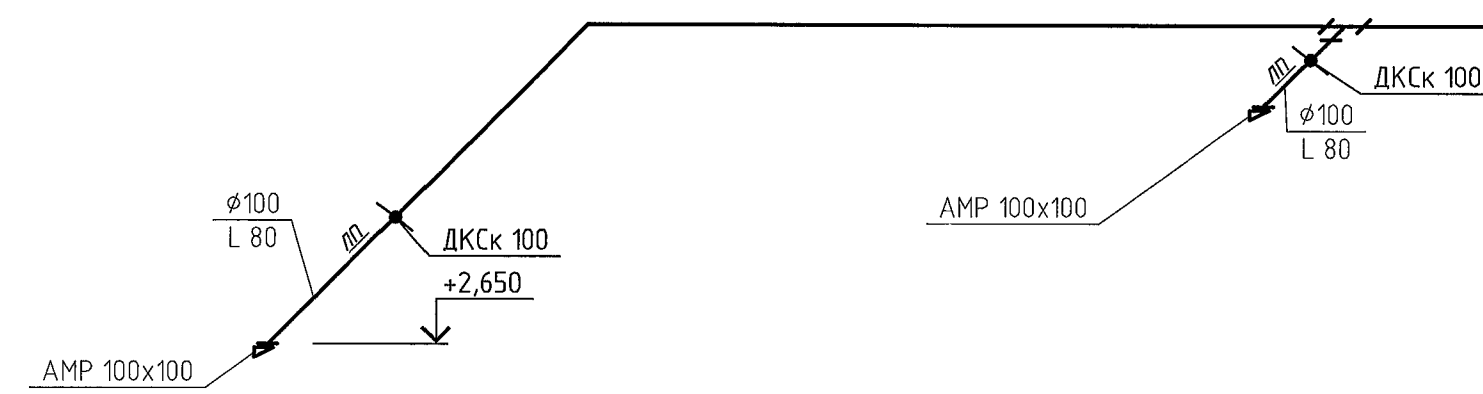


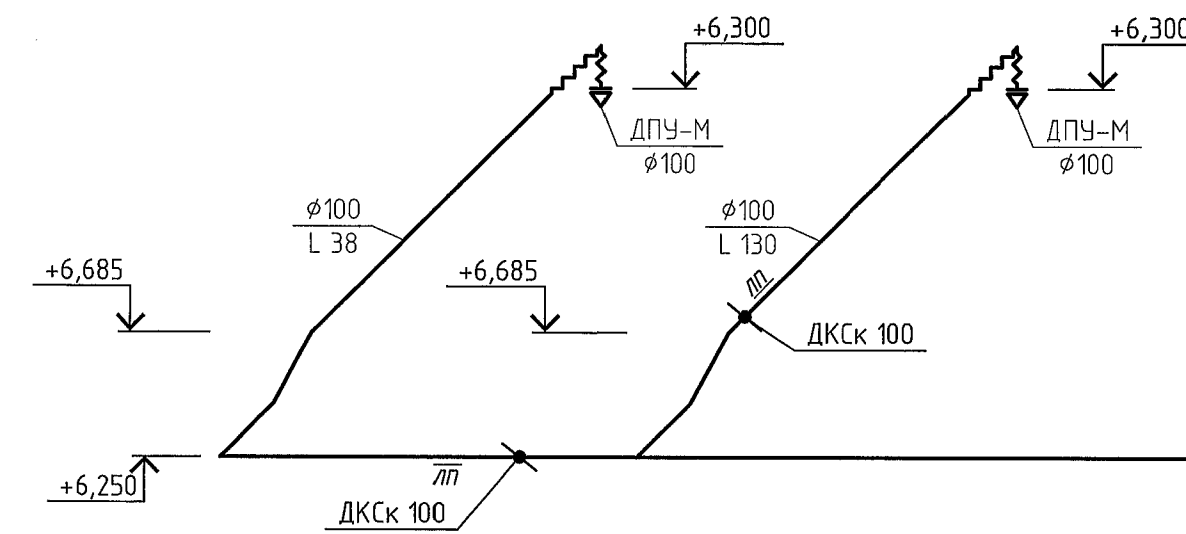

						4570P.D5-100.P.03.BЖК.1.10B.000			
						Магистральный газопровод "Сила Сибири", Этап 5.1. Компрессорная станция КС-1 "Садьякельская"			
Изм.	Км.уч.	Лист	№ док.	Повп.	Дата	Вахтовый жилой комплекс при КС-1 "Садьякельская". Объехитые на 120 мет.	Стадия	Лист	Листов
Разработал	Продумиков				2019		Р	6	
Проверил	Букин				2019				
Гл. спец.	Нелипович				2019				
						Вентиляция. Схемы систем П1, П2, В1, В2. Разрез 1-1	ПАО "ВНИИГаздобыча"		