




B3

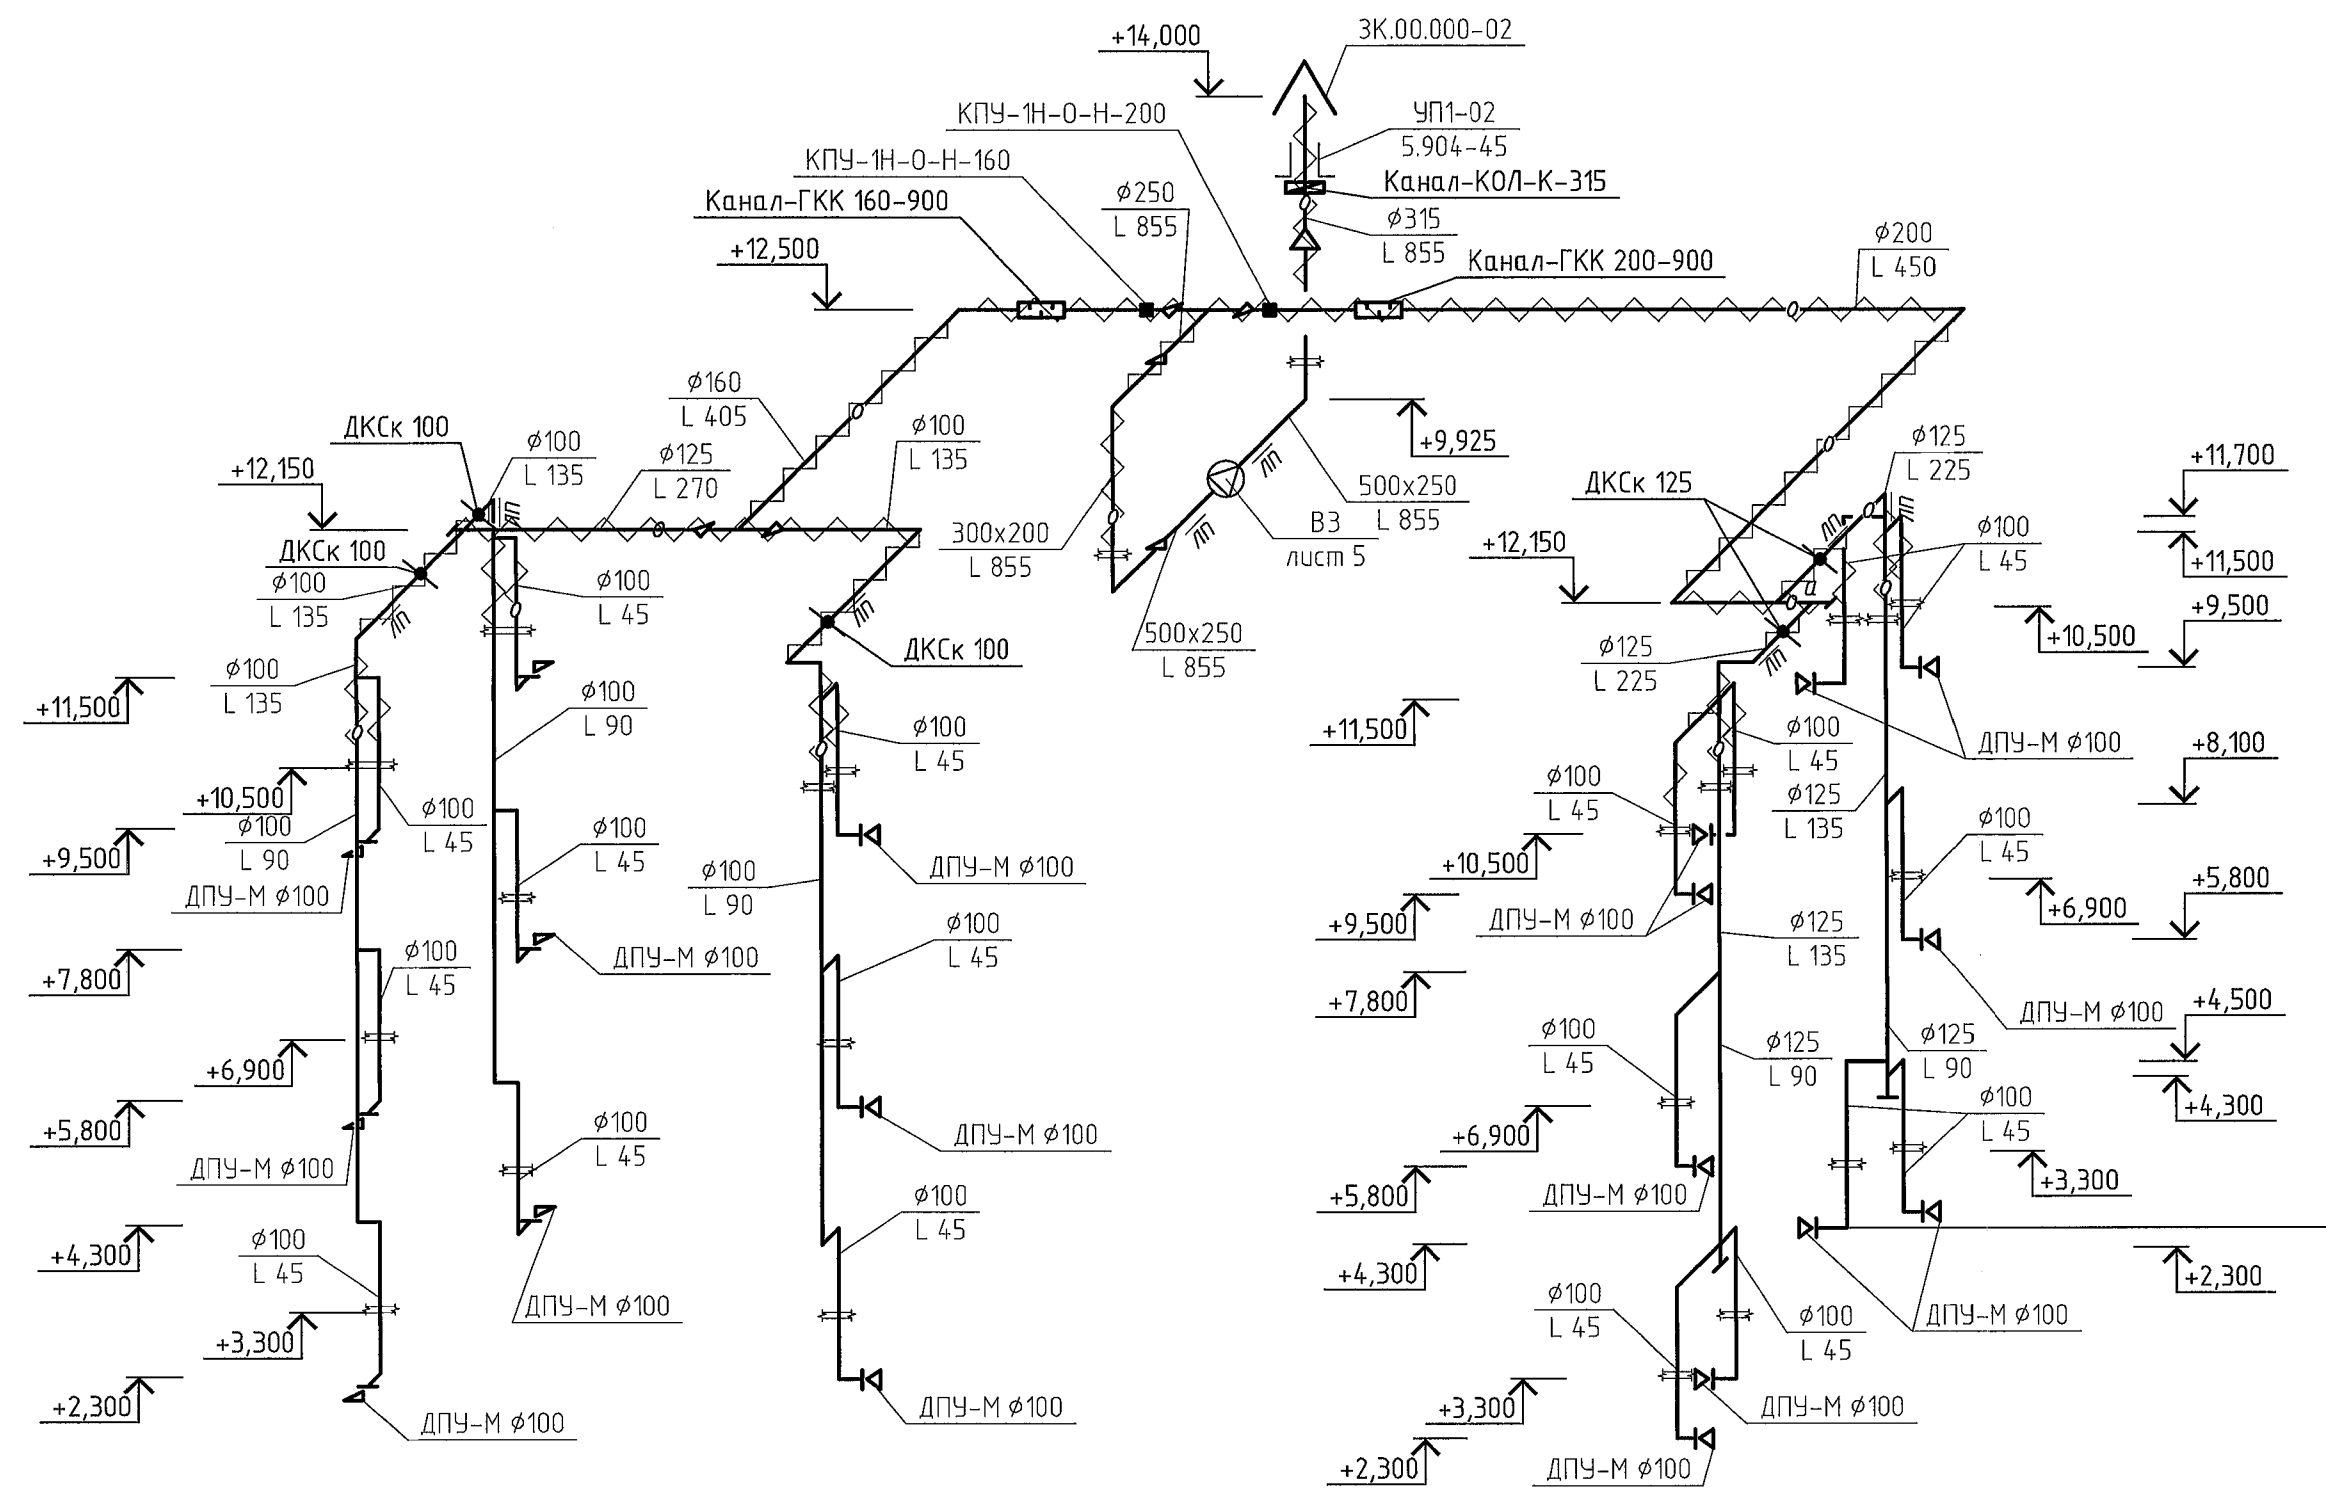


B4

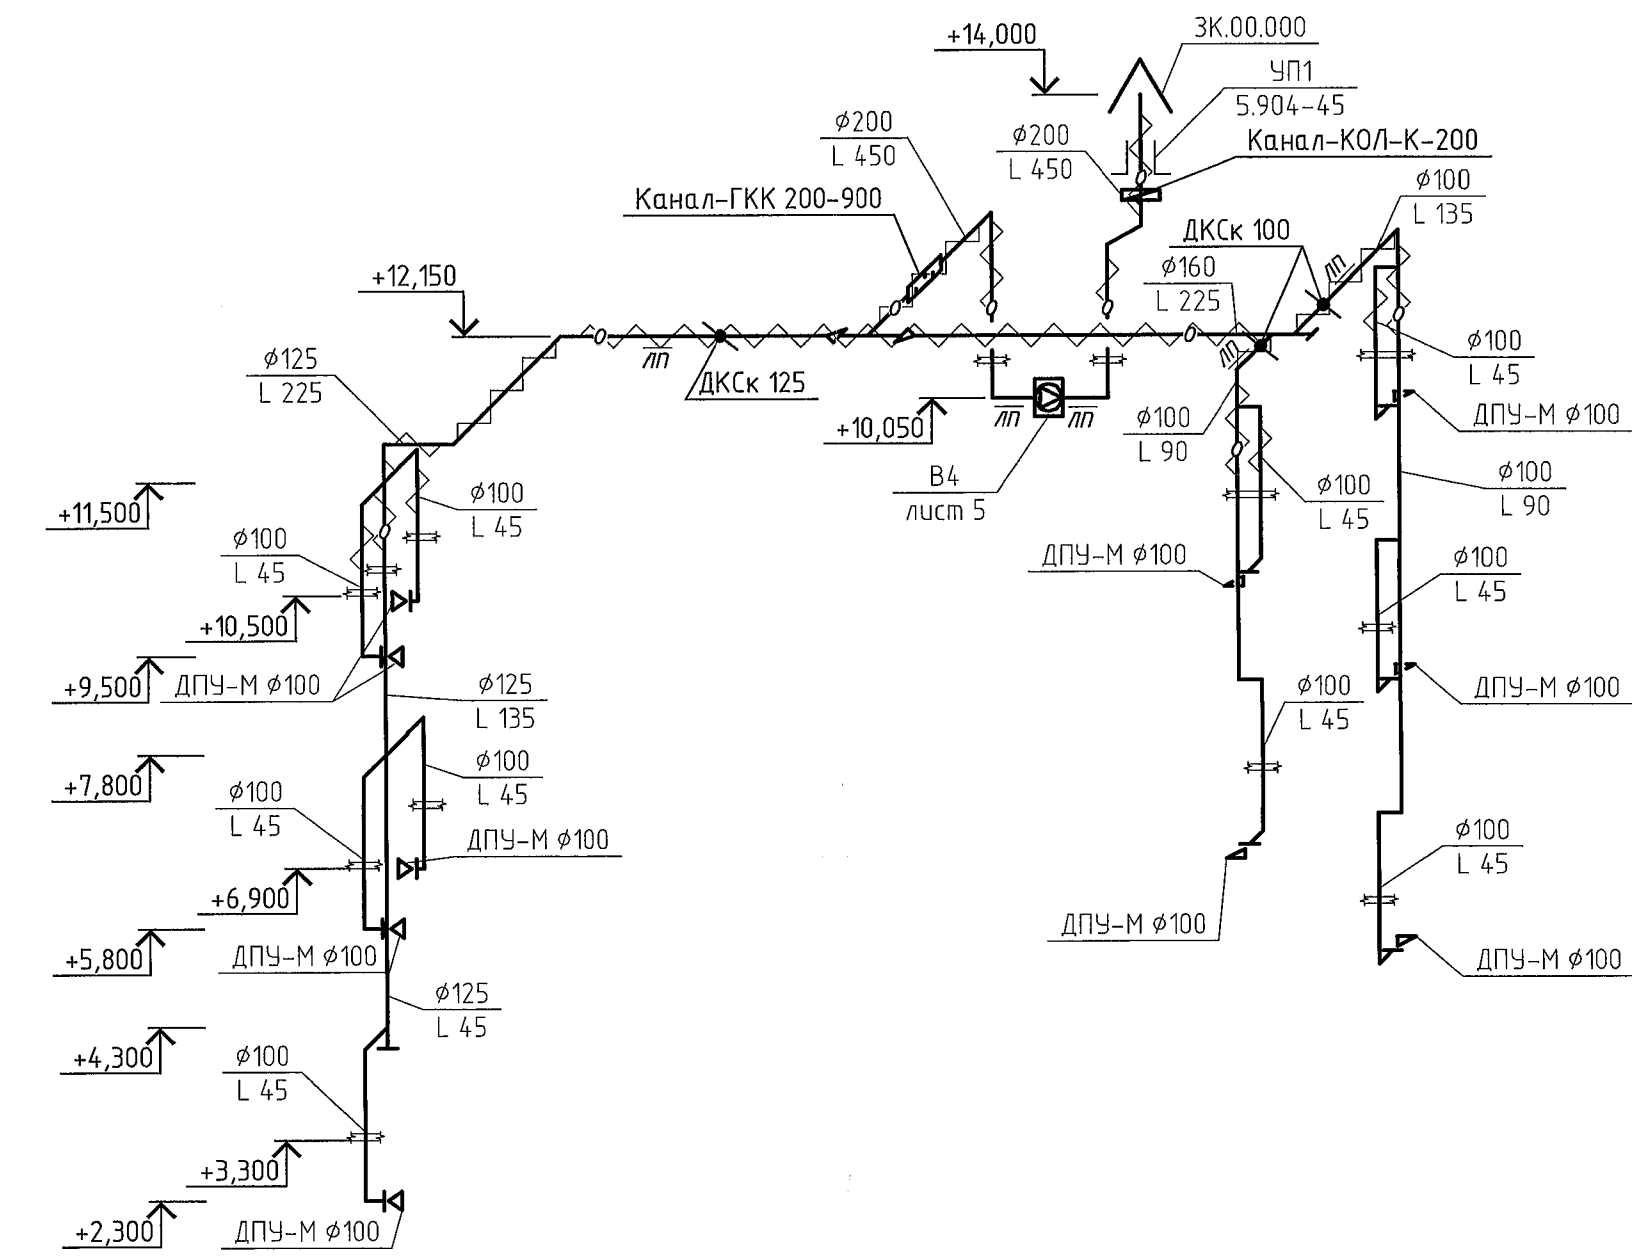

B5

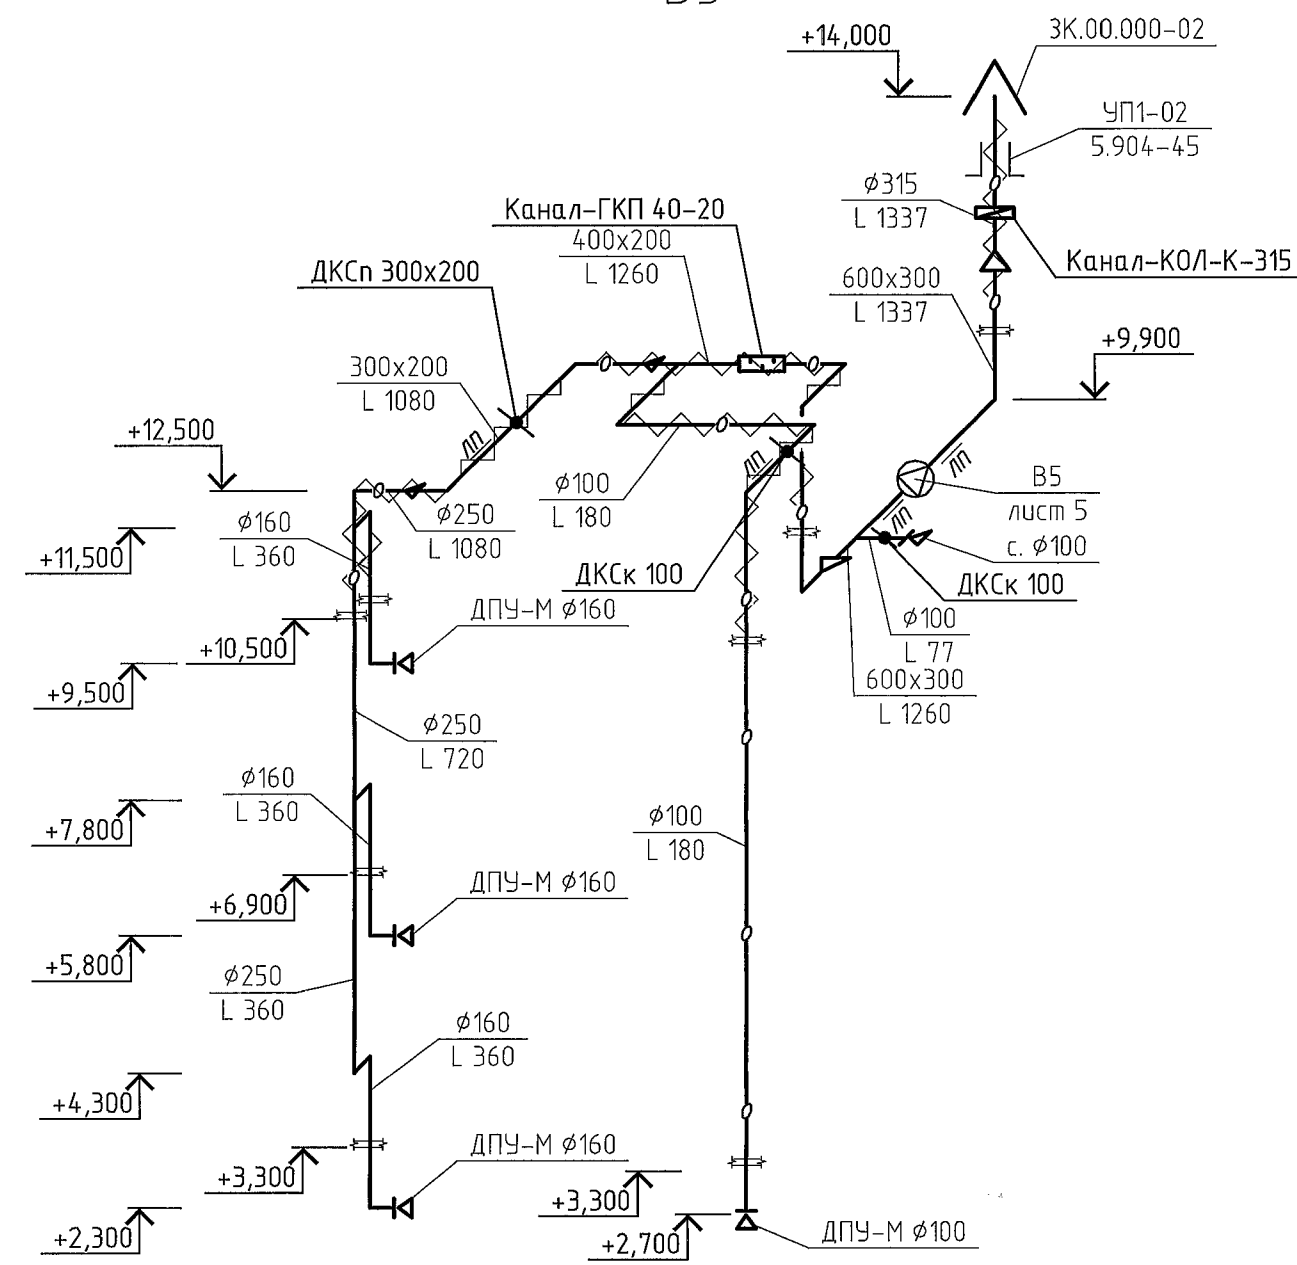

B6

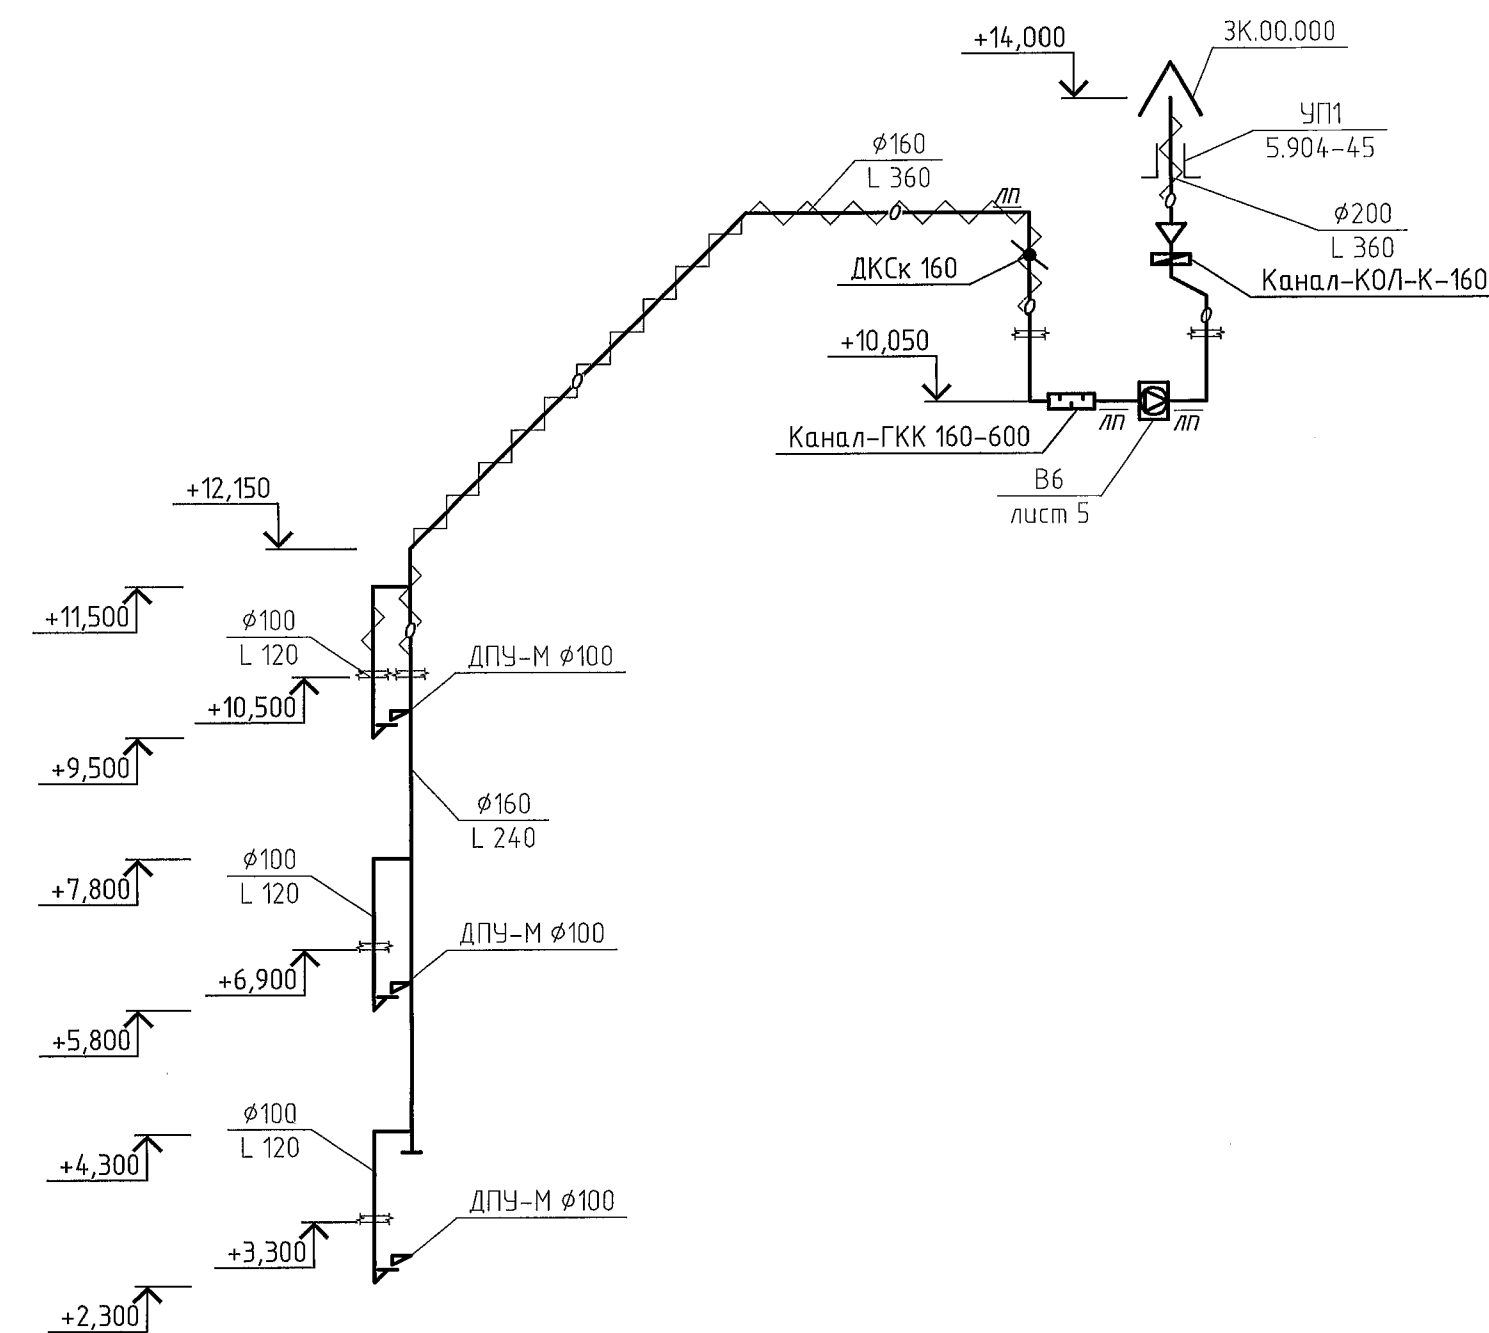

Все воздухопроводы, расположенные на чердаке, выполнены из стали $\delta=1,2$ мм на сварке и покрыты теплобой изоляцией, обеспечивающей предел огнестойкости EI30.

					4570PД5-1.00.P.03.BЖК.1.1.OB.000
					Магистральный газопровод "Сила Сибири". Этап 5.1. Компрессорная станция КС-1 "Салдыкельская"
Изм.	Колич.	Лист	N док.	Подп.	Дата
Разработа		Прудников		[подпись]	
Проверил		Букин		[подпись]	
Гл. спец.		Неплюгович		[подпись]	
Вахтовый жилой комплекс при КС-1 "Салдыкельская". Общешитие на 120 мест					Стандия
					Lист
Вентиляция. Схемы систем ВЗ-В6					P 7
					Lистоб
					ПАО "ВНИПИгаздобыча"

Копирова л

A1

Инв. № подл	Подп. и дата	Взам. инв. №
900581		