

Схема расположения элементов
лестниц Л1 на отм. 0,000

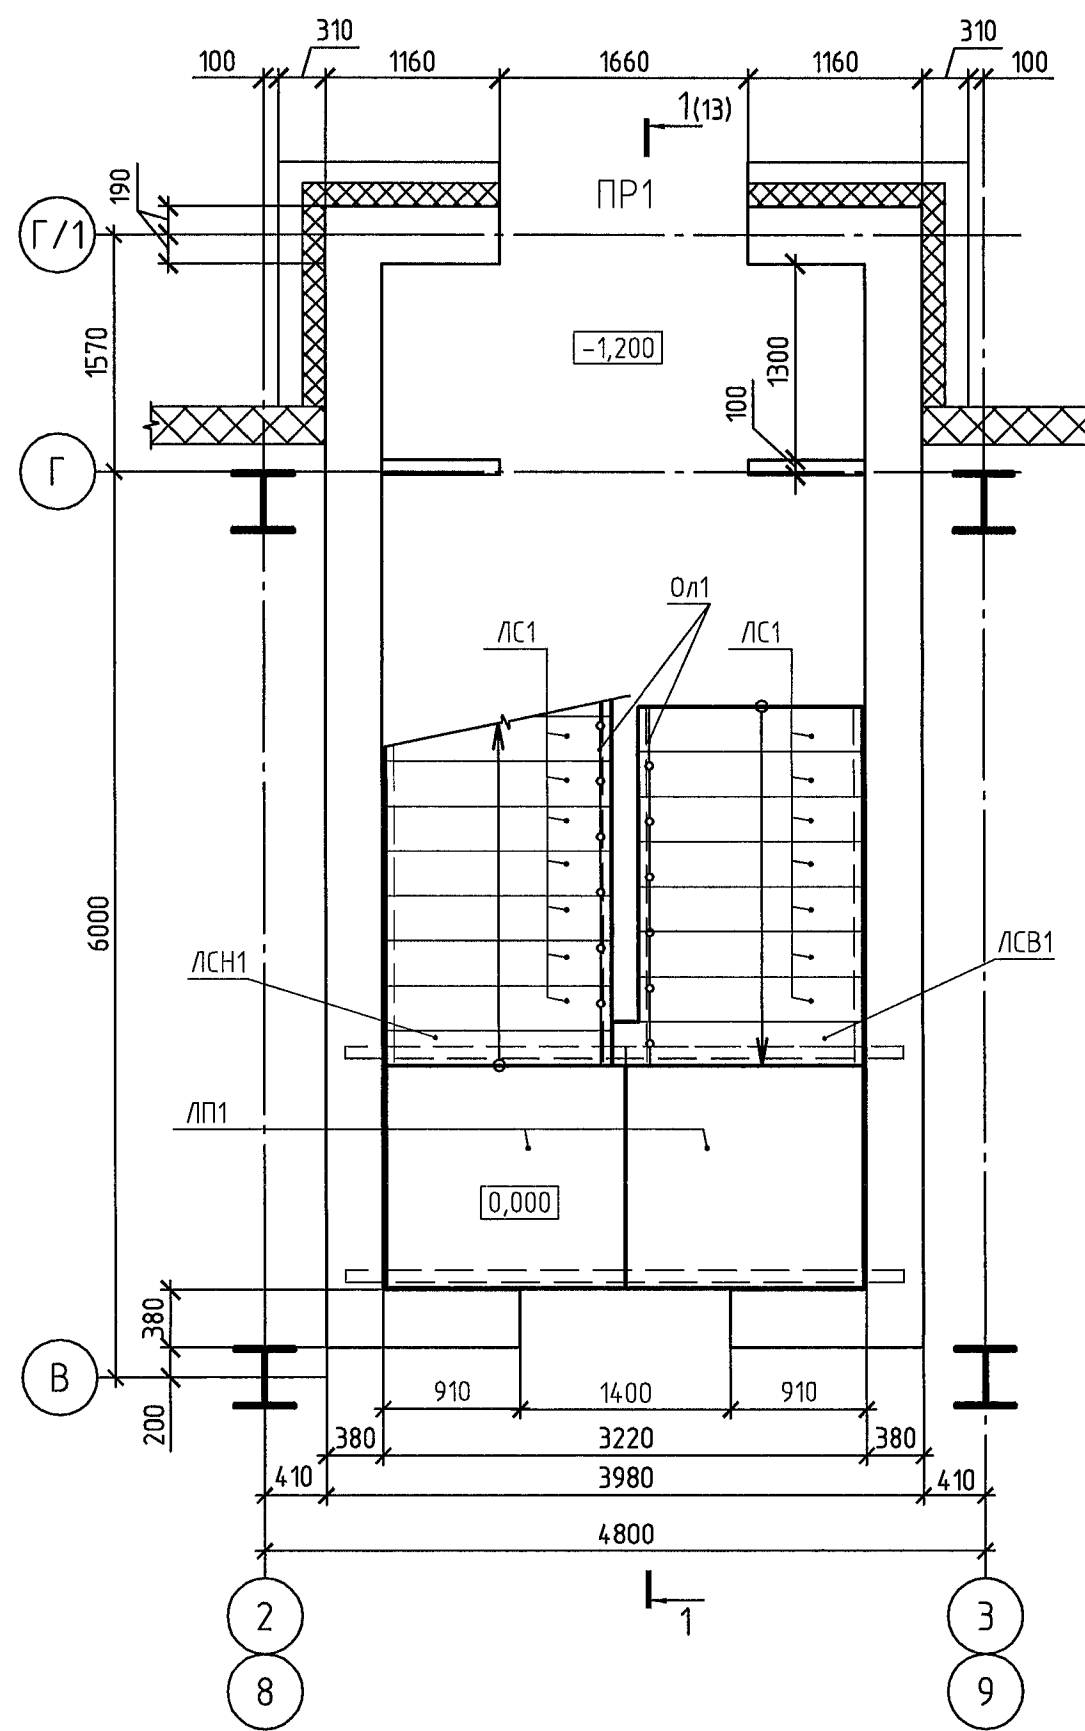


Схема расположения элементов
лестниц Л1 на отм. +3,600

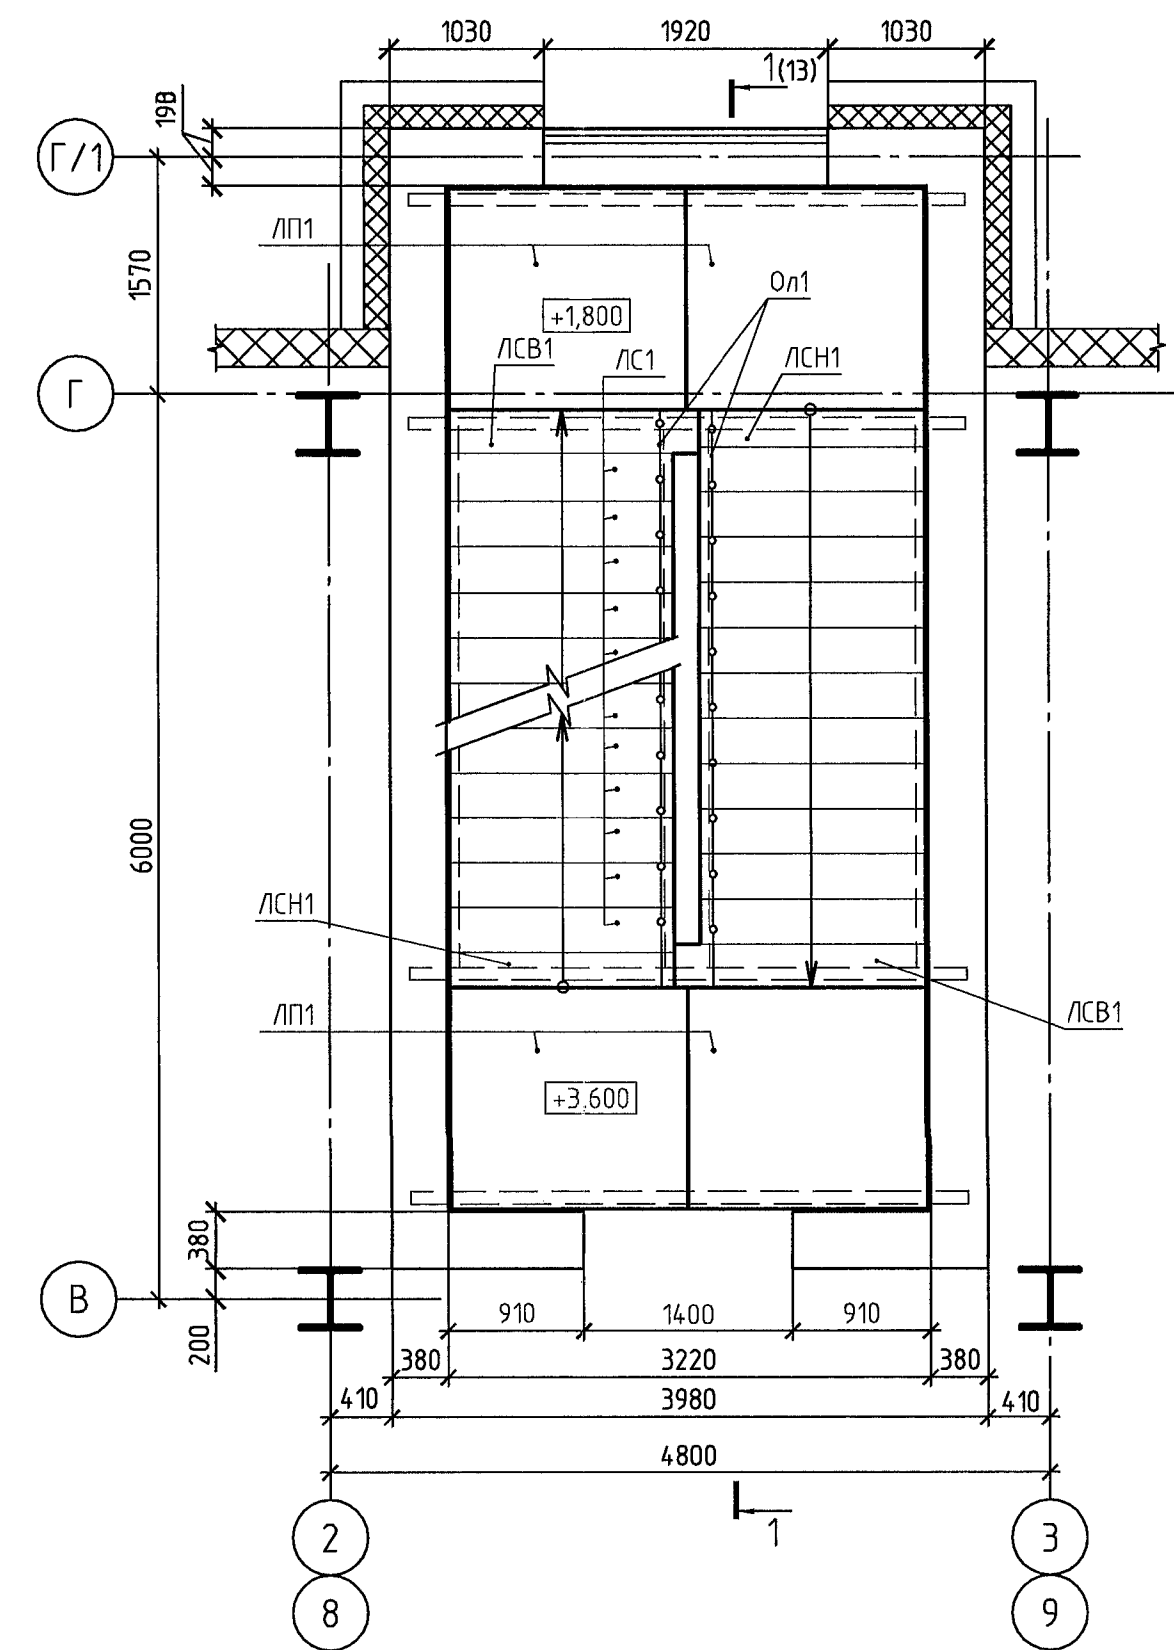


Схема расположения элементов
лестниц Л1 на отм. +7,200




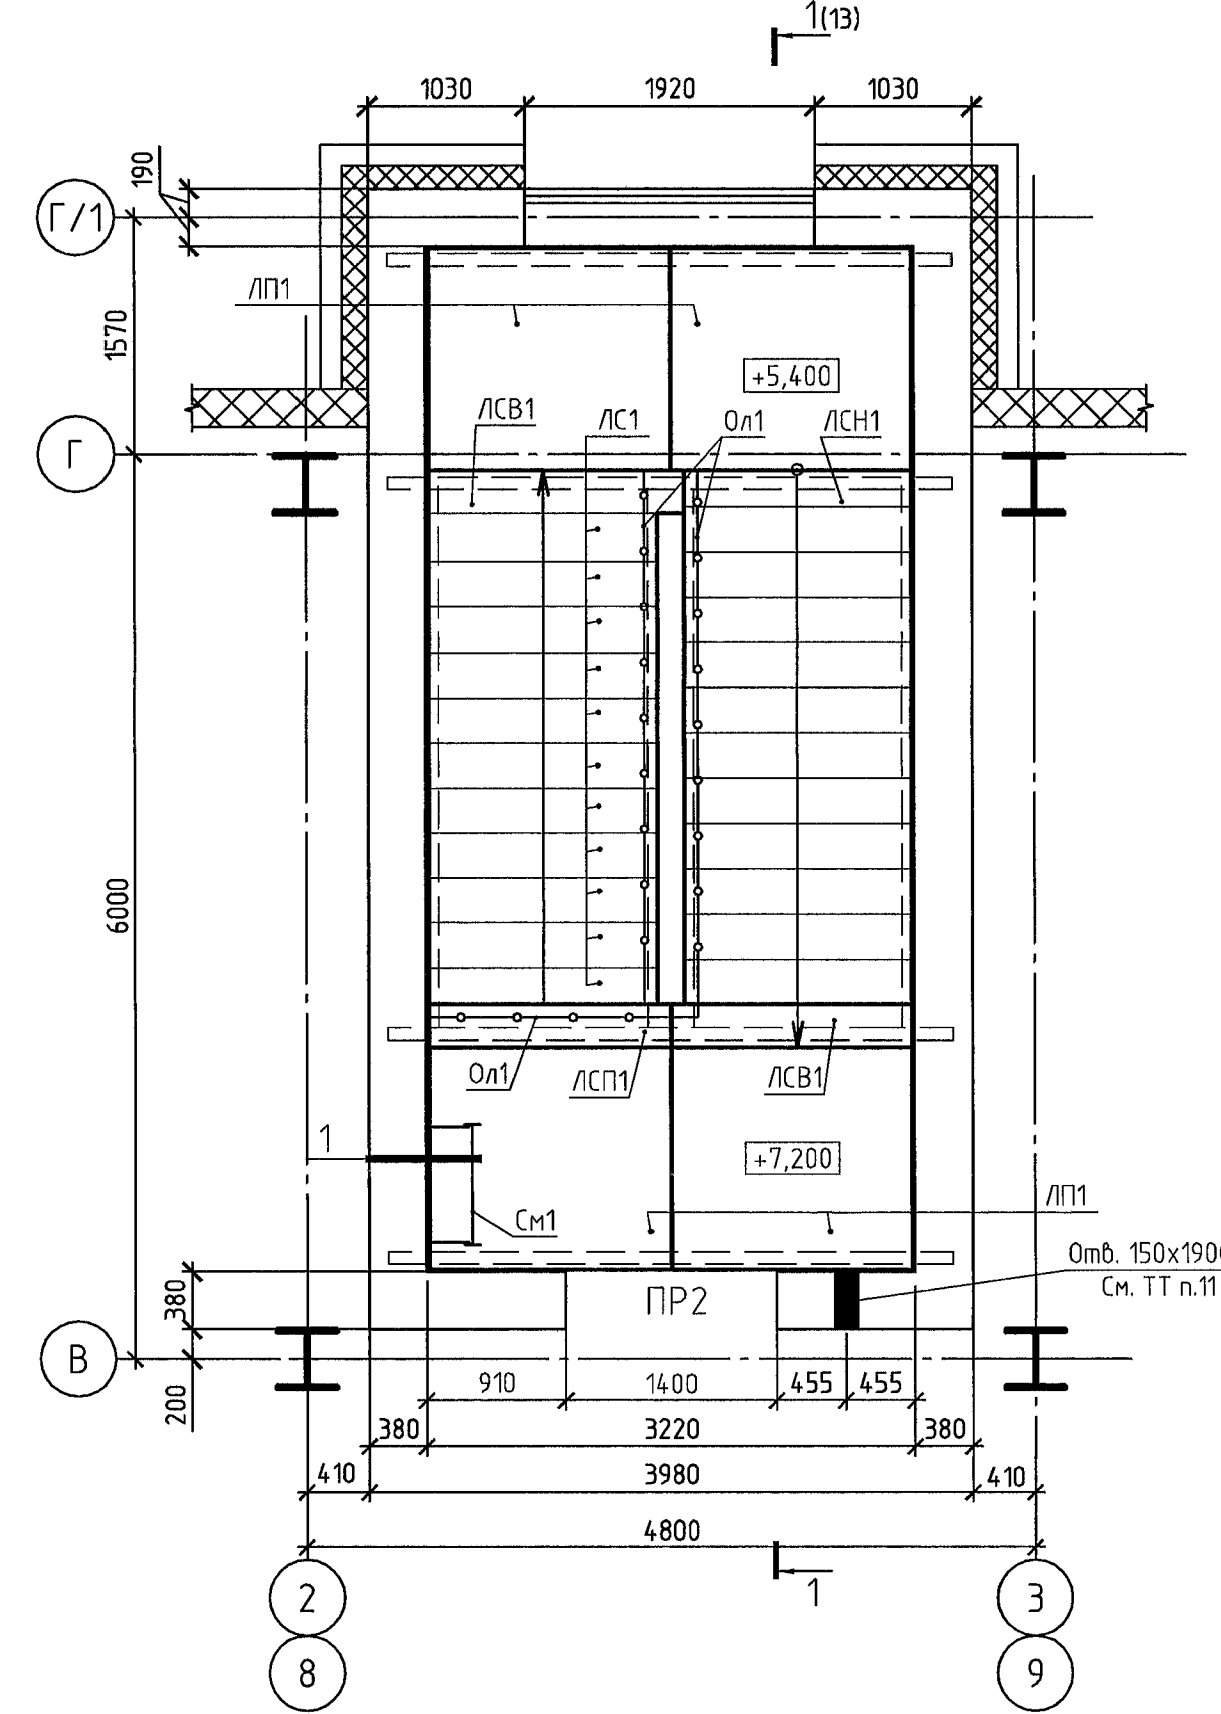


Схема расположения утепления
лестниц Л1 ниже отм. 0,000

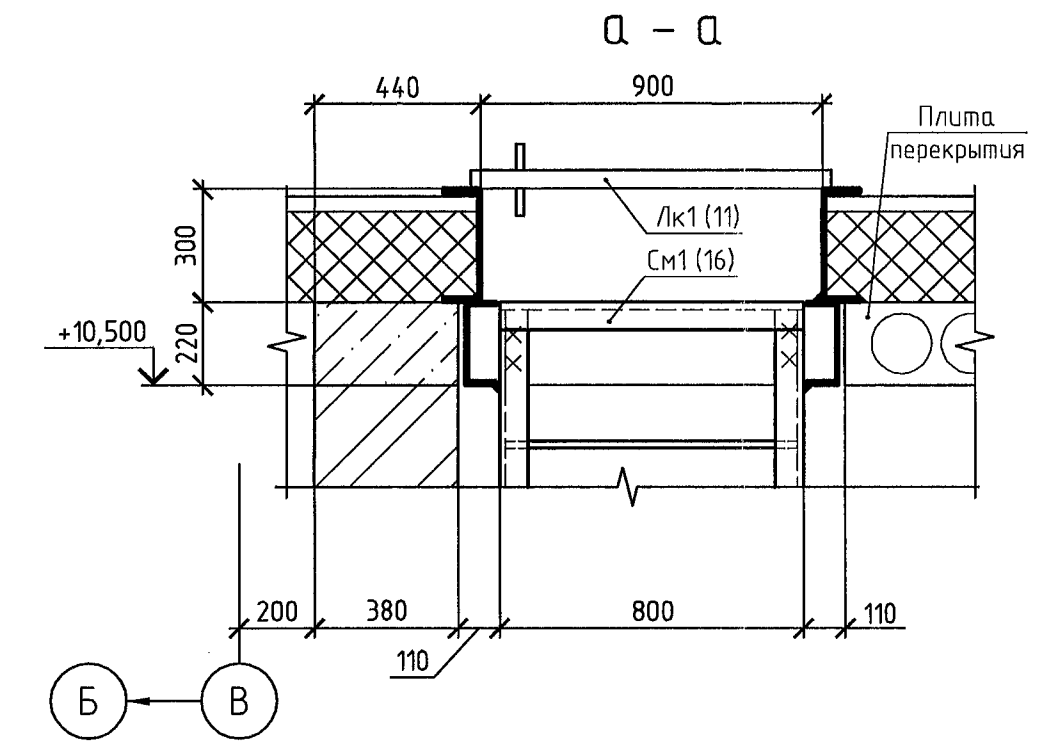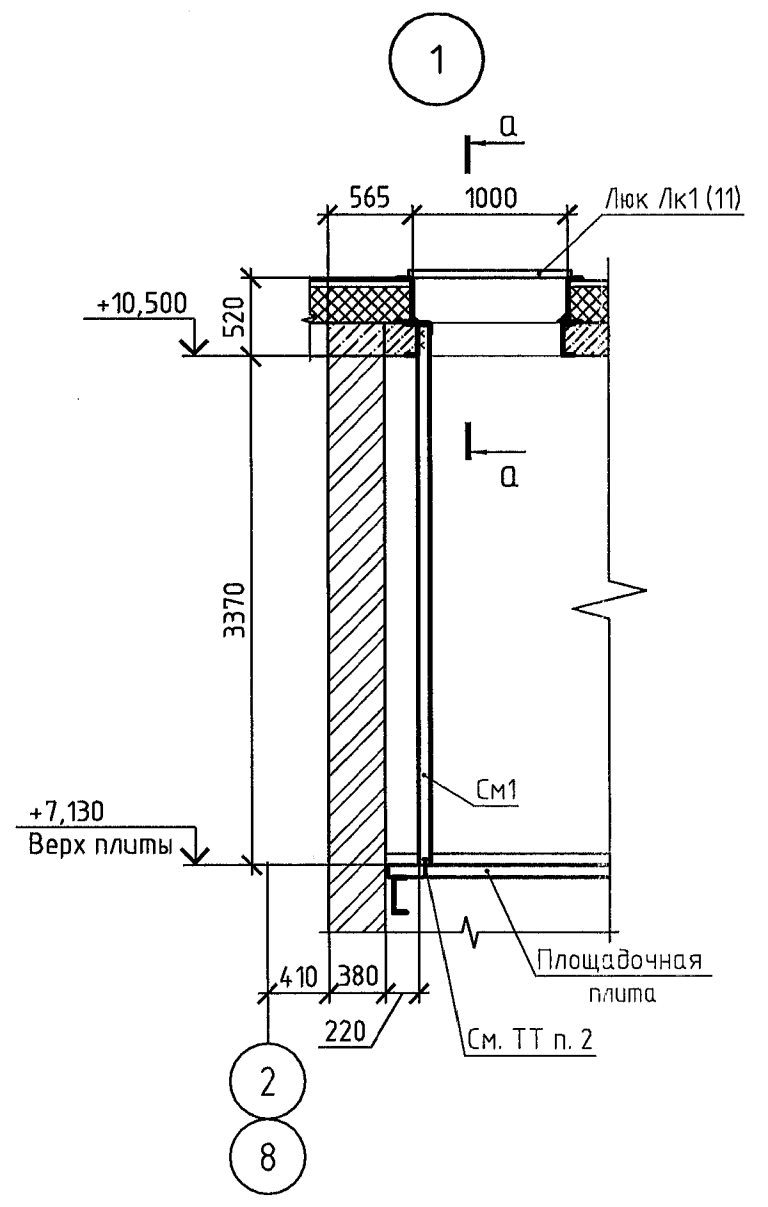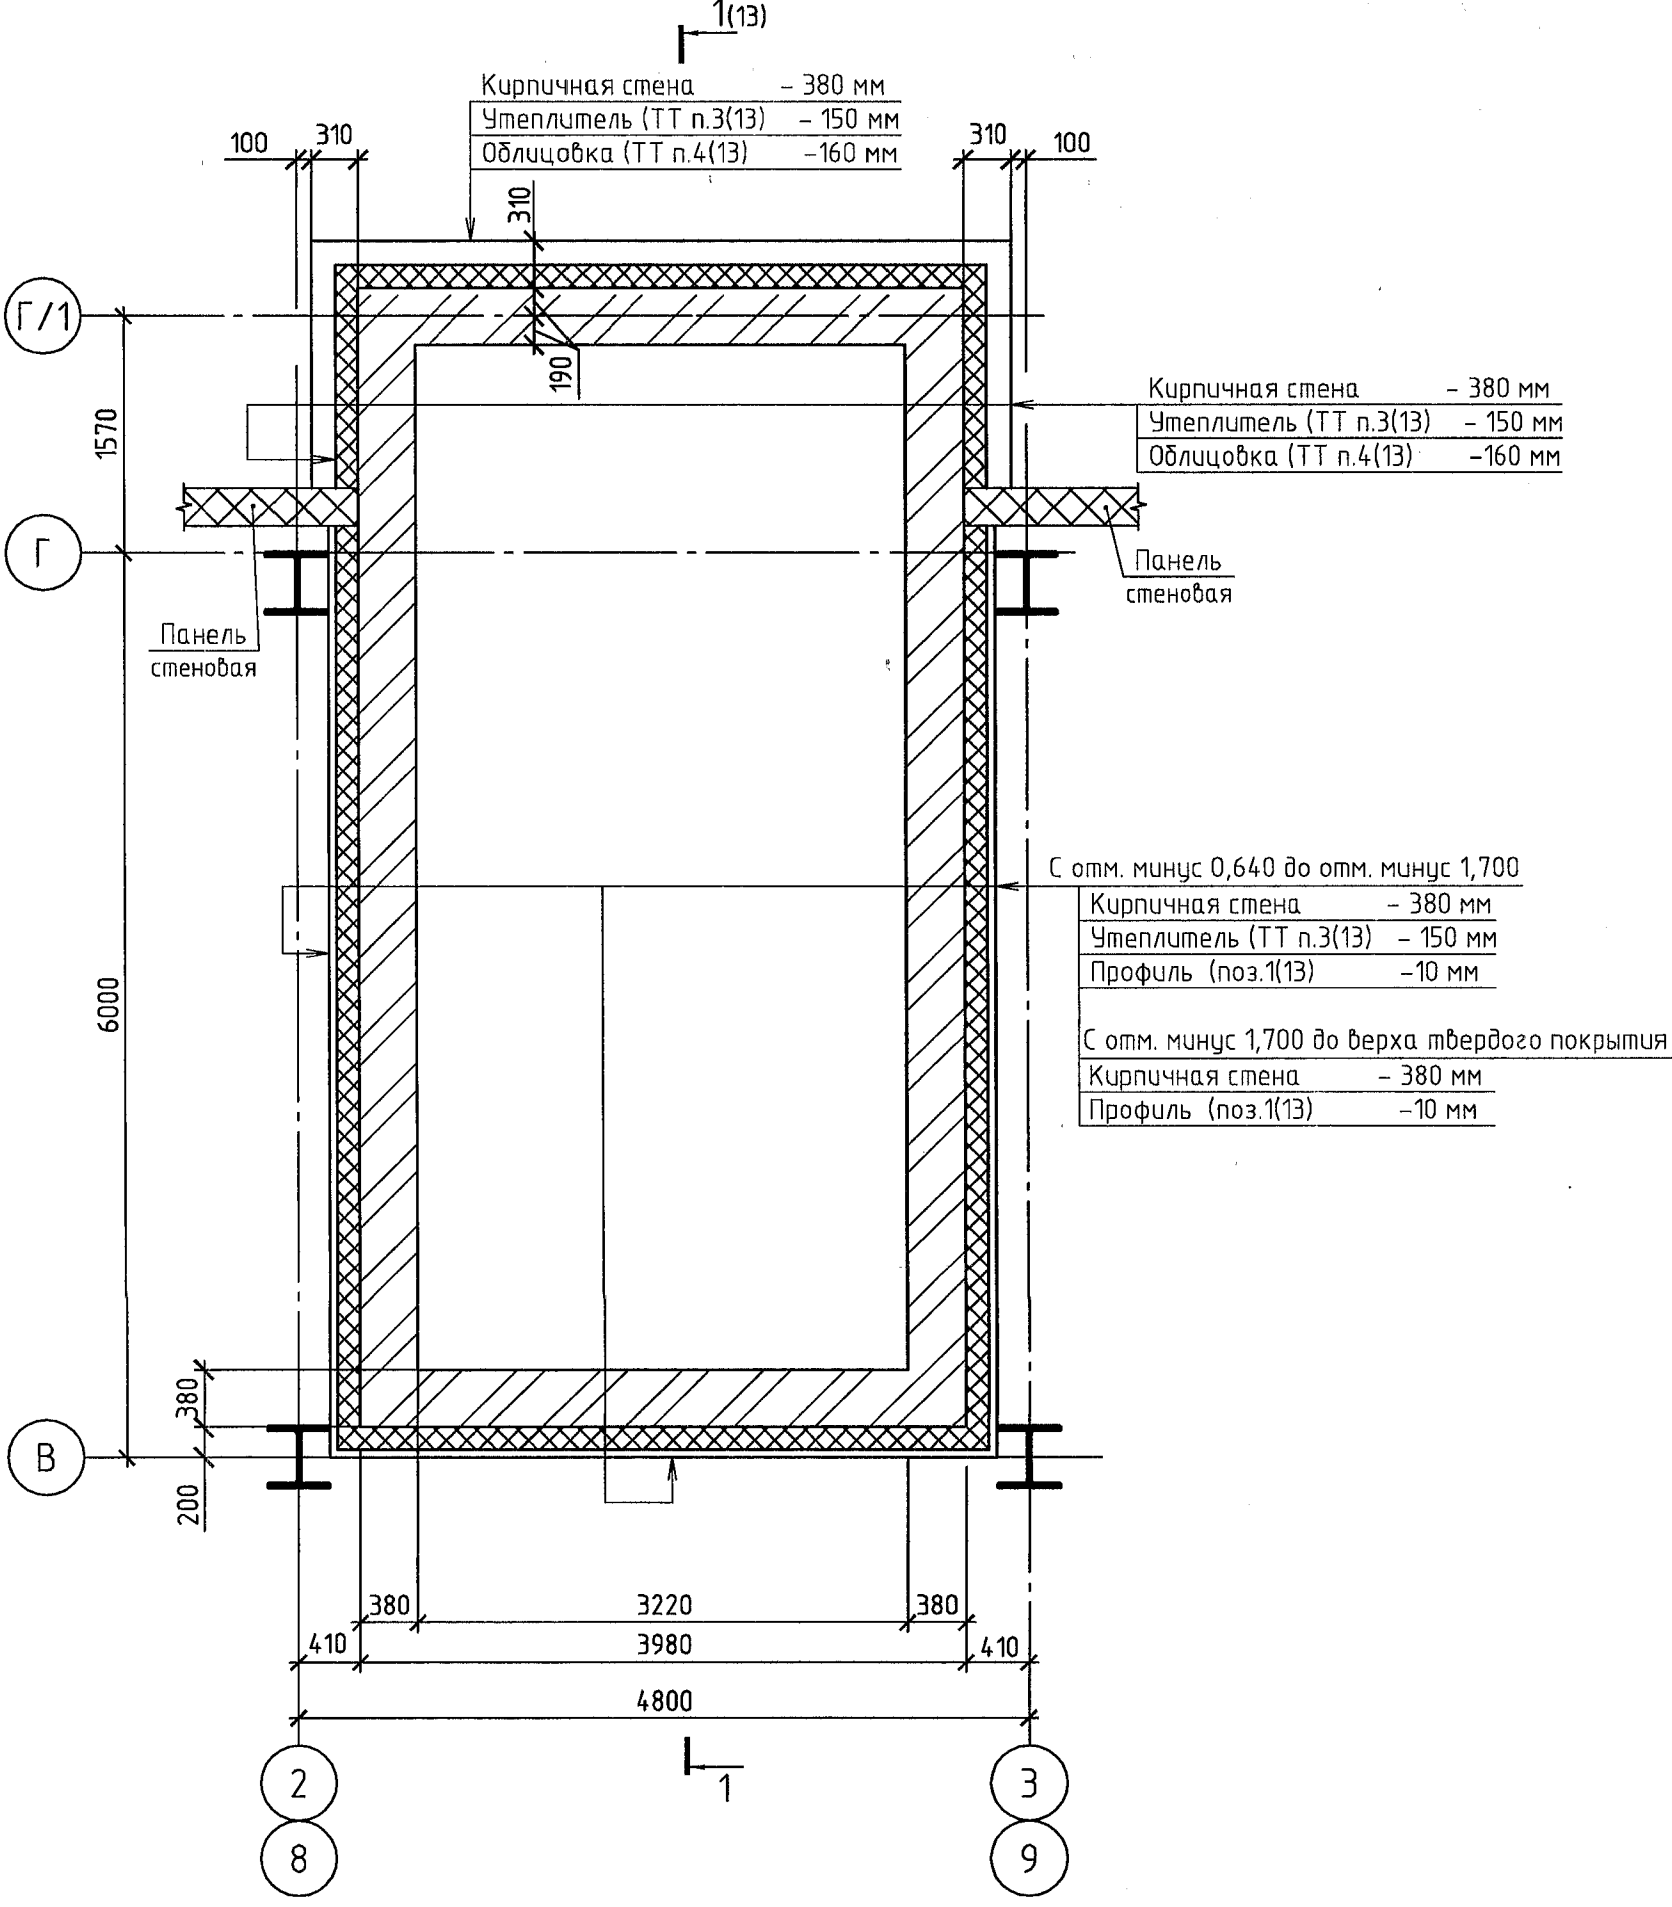

Спецификация к схемам расположения элементов лестниц Л1

Поз.	Обозначение	Наименование	Кол.	Масса ед., кг	Приме- чание
		Ступени			
ЛС1		ЛС 15-1А	51	162,4	
ЛСВ1		ЛСВ 15-А	5	122,1	
ЛСН1		ЛСН 15-А	4	85,4	
ЛСП1		Площадочный вкладыш ЛСП 15-1	1	110,1	
ЛП1		Лист 16	10	545,0	
		Перекрышки			
1		2ПБ 19-3-п	3	81,0	
2		2ПБ 17-2-п	3	71,0	
Ол1		Каталог ООО "СК Стройтекс"	26,0	22,7	м
Сл1		Лист 16	1	72,64	

Ведомость перемычек

Марка	Схема сечения
ПР1 (1 шт.)	
ПР2 (1 шт.)	

- Общие указания по монтажу, сварке и антикоррозионной защите см. лист 1.
- Стремянку Сл1 крепить к площадочной плите анкер-шпиралами НЛС 8х70/40 фирмы НЛТ1.
- Крепление анкерами вести в соответствии с требованиями "Руководства по анкерному креплению" НЛТ1.
- Монтаж ступеней и площадочных плит вести в соответствии с требованиями ГОСТ 8717-2016 и серии 1050.9-4.93 вып.0-1.
- Узлы опирания ж.б. ступеней для сейсмических районов см. серию 1.050.9-4.93 вып.0-1 документ 1050.9-4.93.0-1-8.
- Схемы расположения косяков, балок для опирания площадочных плит и балок покрытия см. лист 15.
- Крепление и монтаж ограждений лестничных маршей и площадок вести в соответствии с требованиями и рекомендациями ООО "СК Стройтекс".
- Узлы по огнезащите металлических конструкций лестницы Л1 см. лист 15.
- Схемы расположения плит перекрытия лестницы Л1 см. лист 11.
- Монтаж перемычек (поз.1,2) вести в соответствии с требованиями СП 16.13330.2016 и серии 1038.1-1 вып.1 на свежесделанный раствор М50, Г42 по ГОСТ 28013-98*. Перемычки выполнять из бетона с маркой по морозостойкости F150.
- Расход в спецификации дан на одну лестницу Л1, общее количество лестниц Л1 - 2 шт.
- Предусмотреть отверстие в стене под кабельный ввод (см. чертеж), низ отверстия на отм. +9,700. Отверстие выполнить только для лестничной клетки между осями 2 и 3.

4570РД5-1.00.Р.03.ВЖК.1.1.АС.000					
Магистральный газопровод "Сила Сибири". Этап 5.1. Компрессорная станция КС-1 "Салдыжельская"					
Изм.	Кол. изм.	Лист	№ док.	Подп.	Дата
Разраб.	Плохова	1	18.01.19		
Проб.	Клинов	1	18.01.19		
Гл. спец.	Белов	1	18.01.19		
Вахтовый жилой комплекс при КС-1 "Салдыжельская". Общественные на 120 мест				Стadia	Лист
Схемы расположения утепления лестниц Л1 ниже отм. 0,000 и элементов лестниц Л1 на отм. 0,000; +3,600; +7,200				Р	10
Копировал				ПАО "ВНИИГаздобыча"	